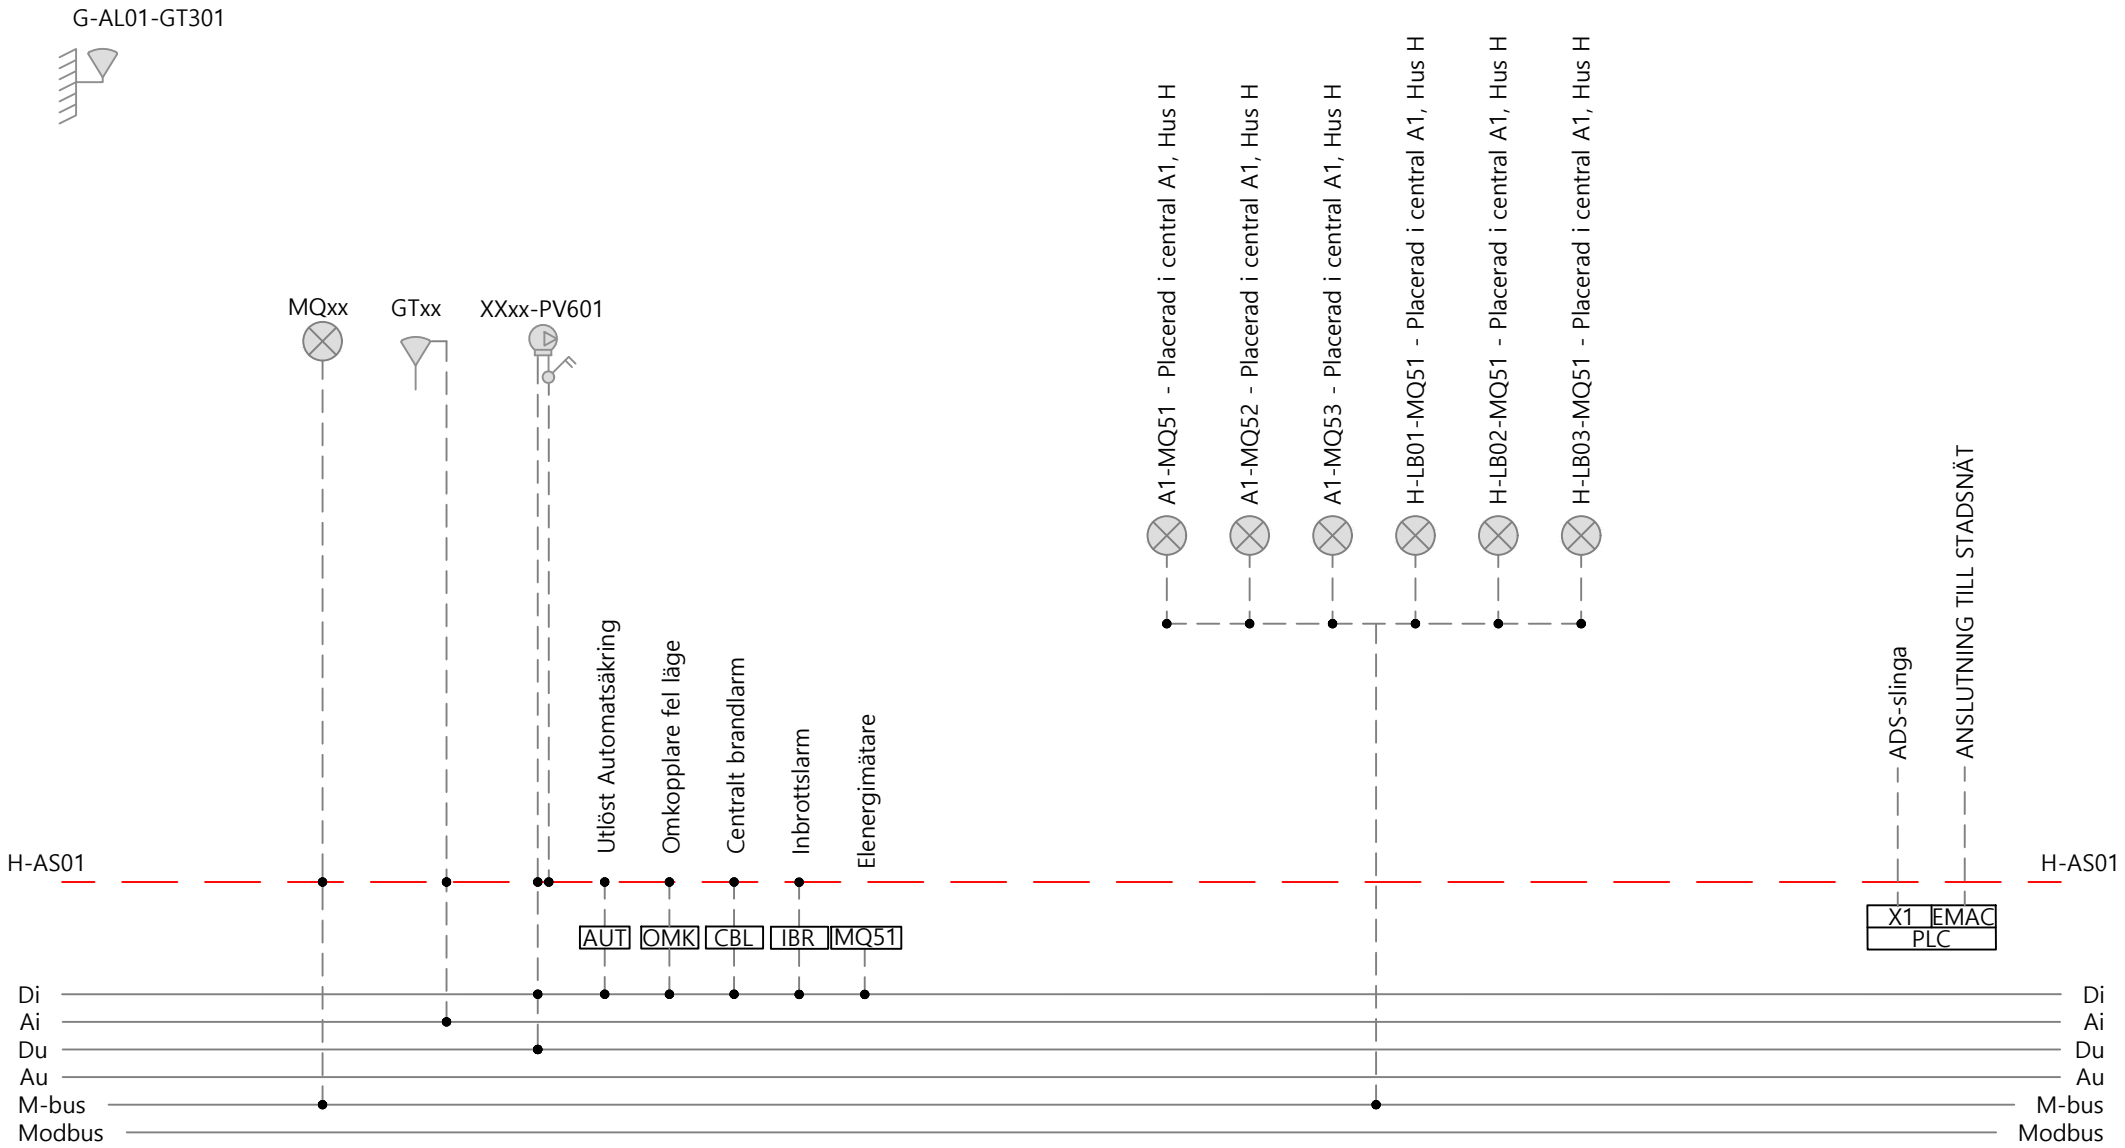
G-AL01-GT301
MQxx
GTxx
XXxx-PV601
Utlöst Automatsäkring
Omkopplare fel läge
Centralt brandlarm
Inbrottslarm
Elenergimätare
A1-MQ51 - Placerad i central A1, Hus H
A1-MQ52 - Placerad i central A1, Hus H
A1-MQ53 - Placerad i central A1, Hus H
H-LB01-MQ51 - Placerad i central A1, Hus H
H-LB02-MQ51 - Placerad i central A1, Hus H
H-LB03-MQ51 - Placerad i central A1, Hus H
ADS-slinga
ANSLUTNING TILL STADSNÄT
H-AS01
H-AS01
AUT
OMK
CBL
IBR
MQ51
X1
EMAC
PLC
Di
Ai
Du
Au
M-bus
Modbus
Di
Ai
Du
Au
M-bus
Modbus