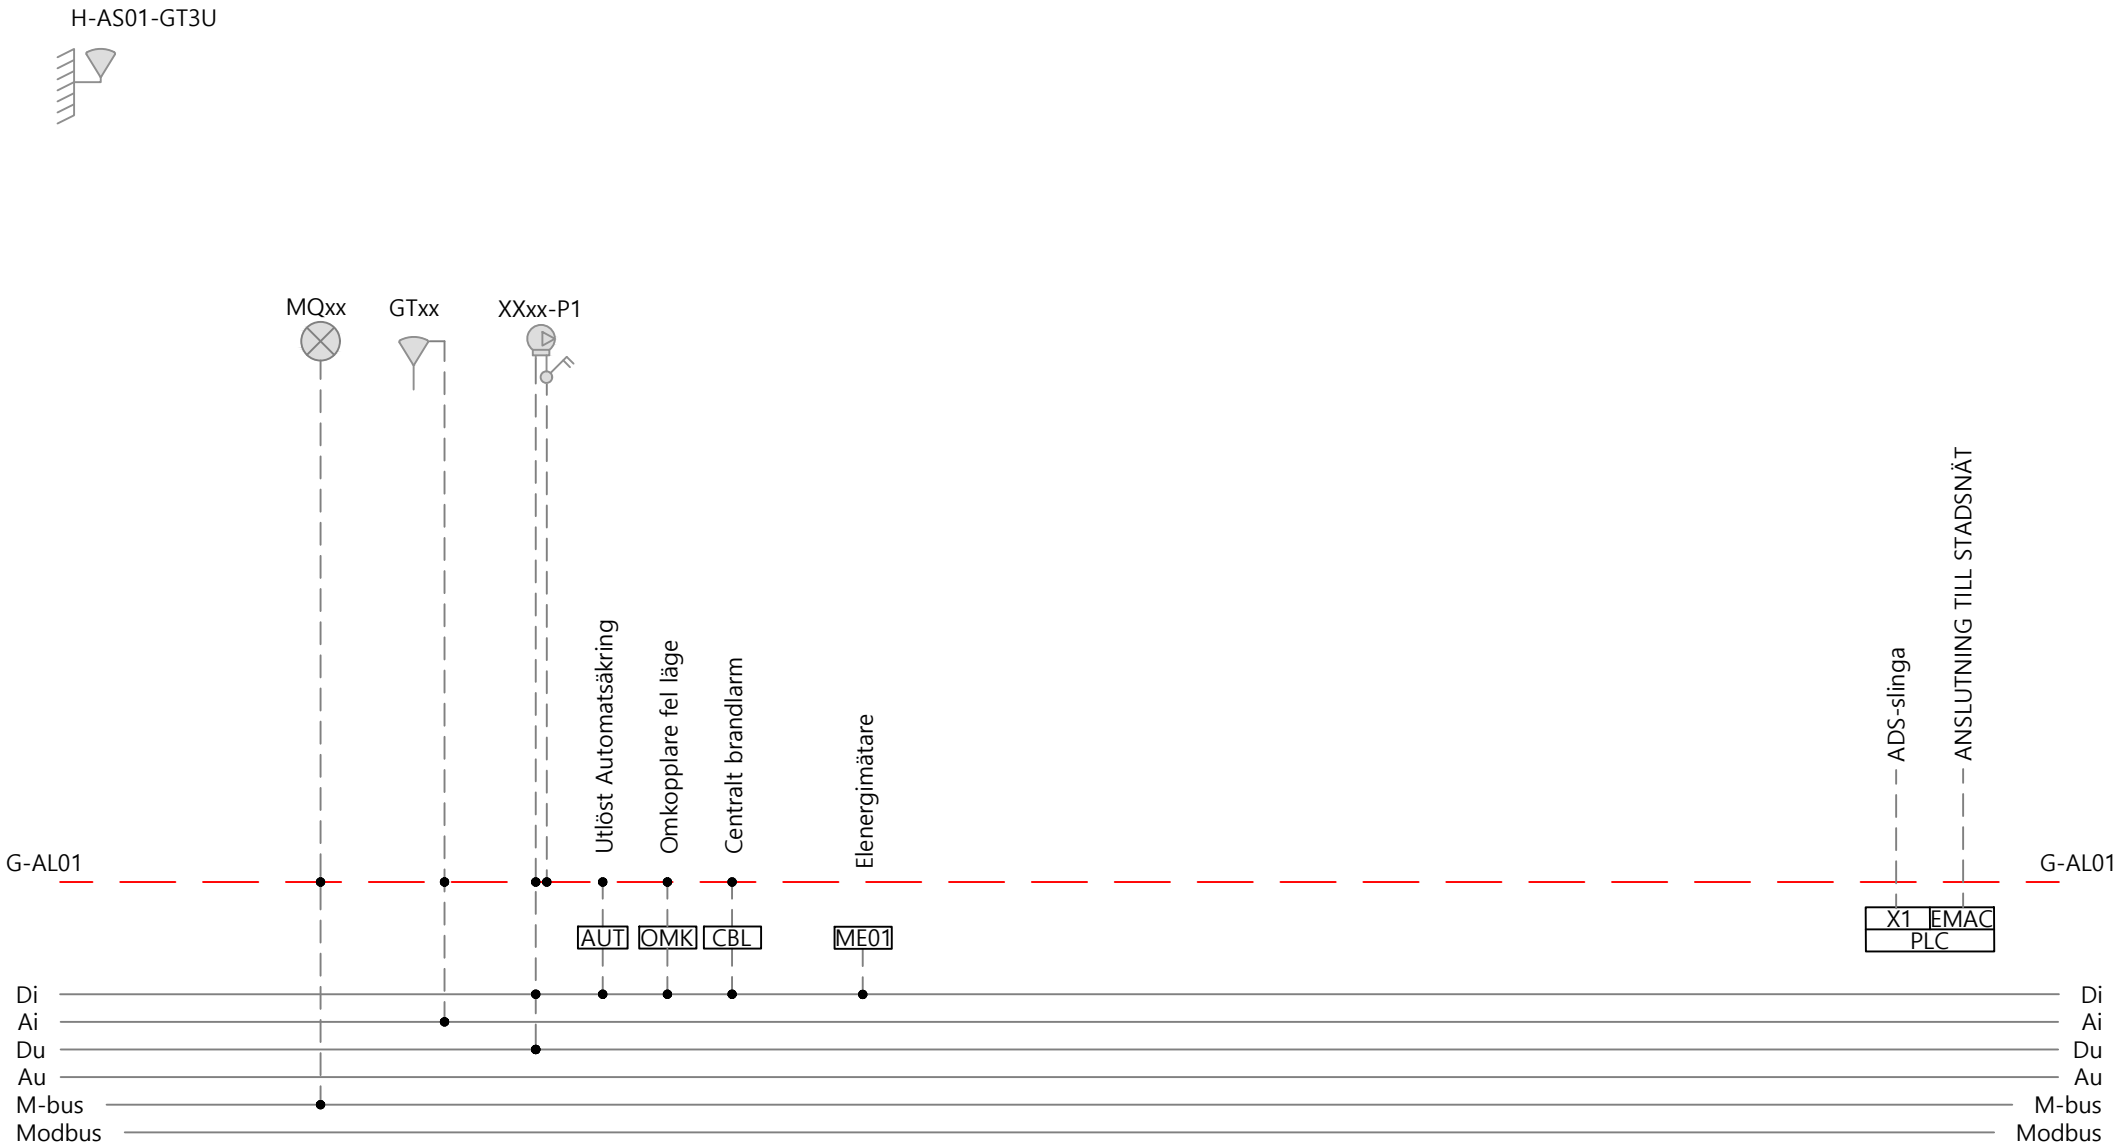
H-AS01-GT3U
MQxx
GTxx
XXxx-P1
Utlöst Automatsäkring
Omkopplare fel läge
Centralt brandlarm
Elenergimätare
ADS-slinga
ANSLUTNING TILL STADSNÄT
G-AL01
G-AL01
AUT
OMK
CBL
ME01
X1
EMAC
PLC
Di
Ai
Du
Au
M-bus
Modbus
Di
Ai
Du
Au
M-bus
Modbus