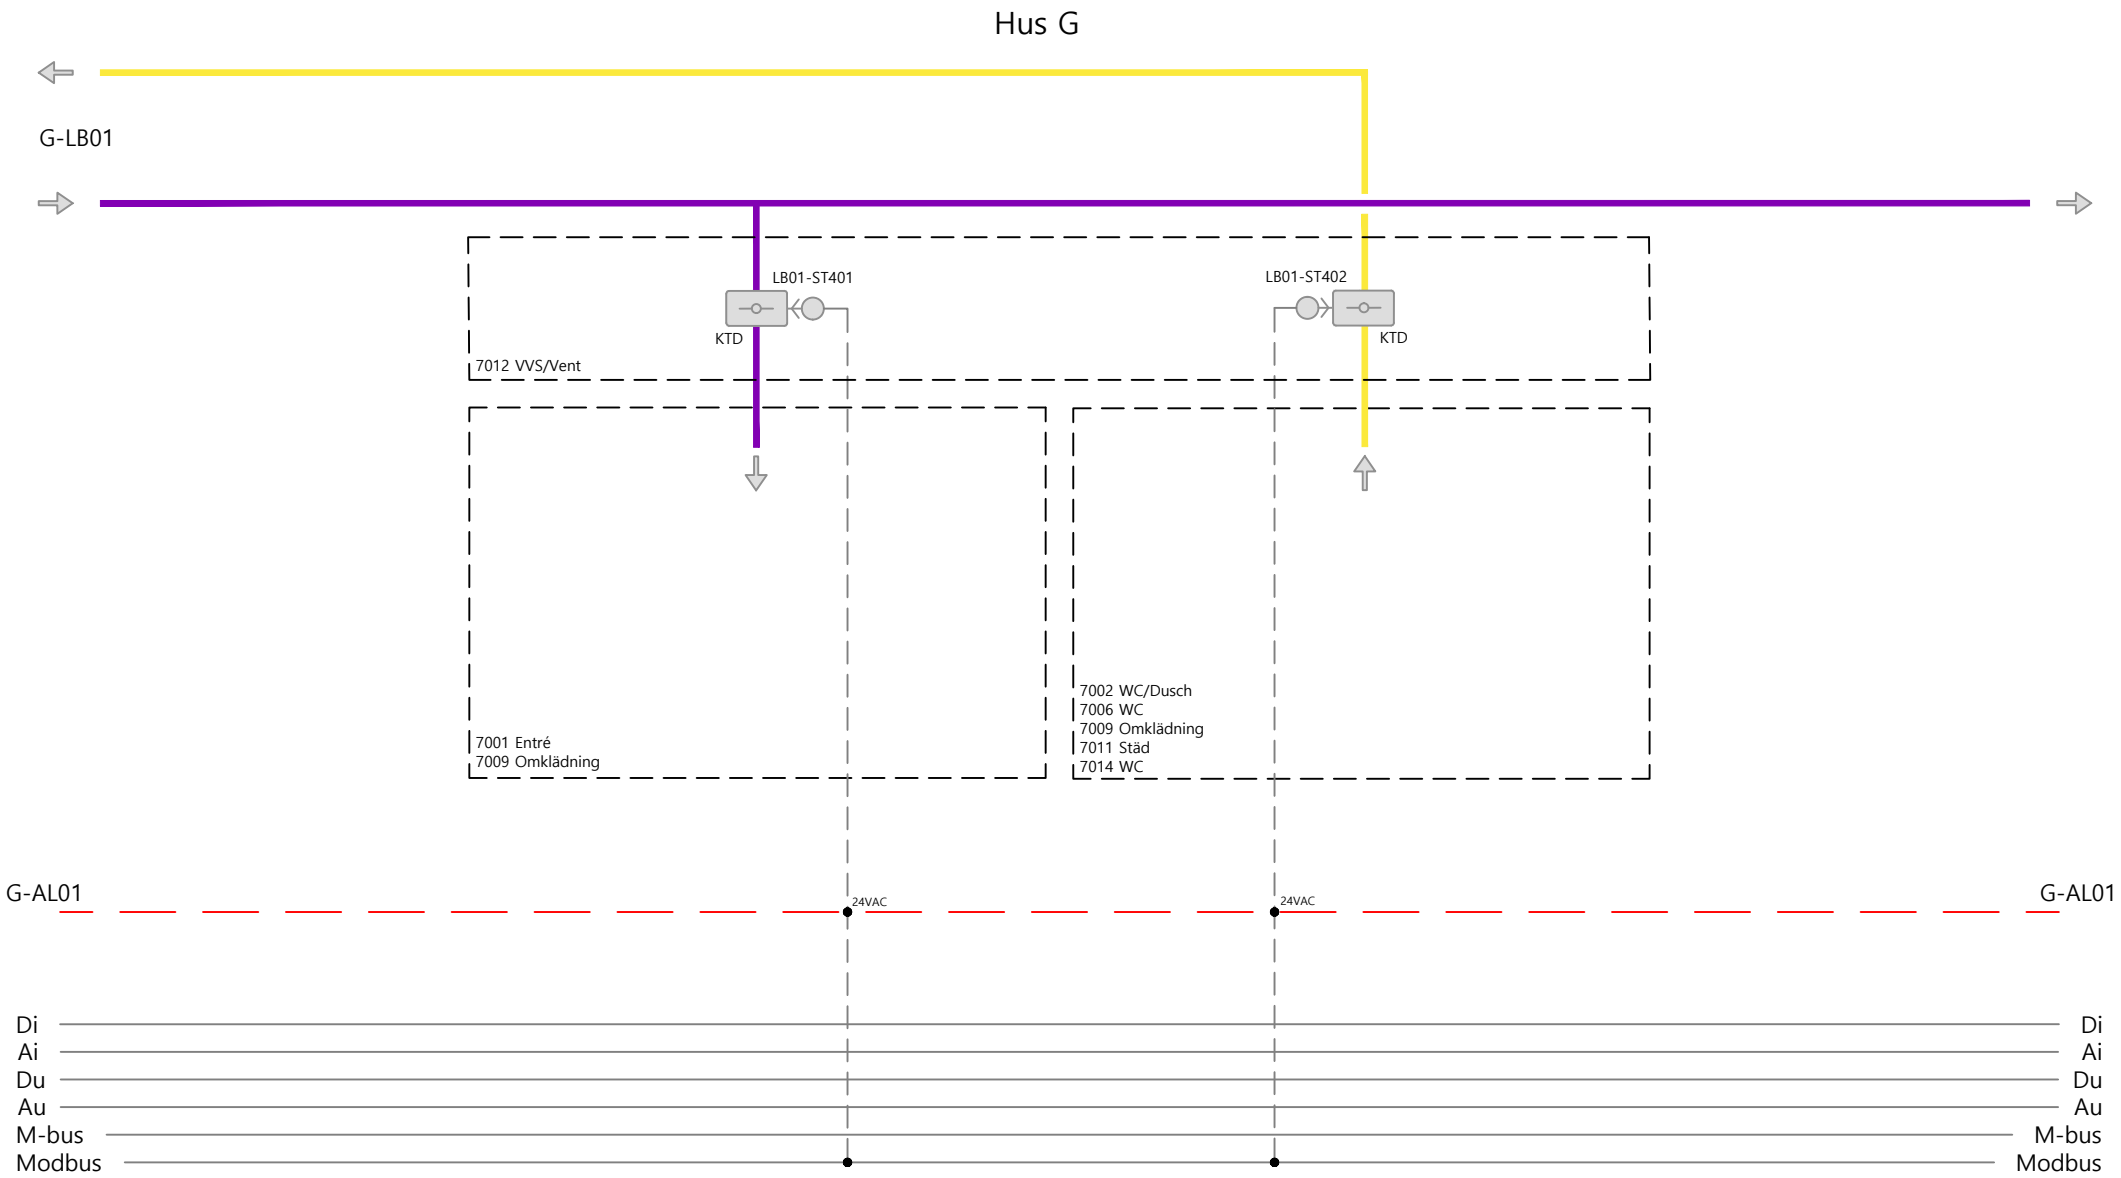
Hus G
G-LB01
LB01-ST401
KTD
LB01-ST402
KTD
7012 VVS/Vent
7001 Entré
7009 Omklädning
7002 WC/Dusch
7006 WC
7009 Omklädning
7011 Städ
7014 WC
G-AL01
24VAC
24VAC
G-AL01
Di
Ai
Du
Au
M-bus
Modbus
Di
Ai
Du
Au
M-bus
Modbus