Hus H plan 10

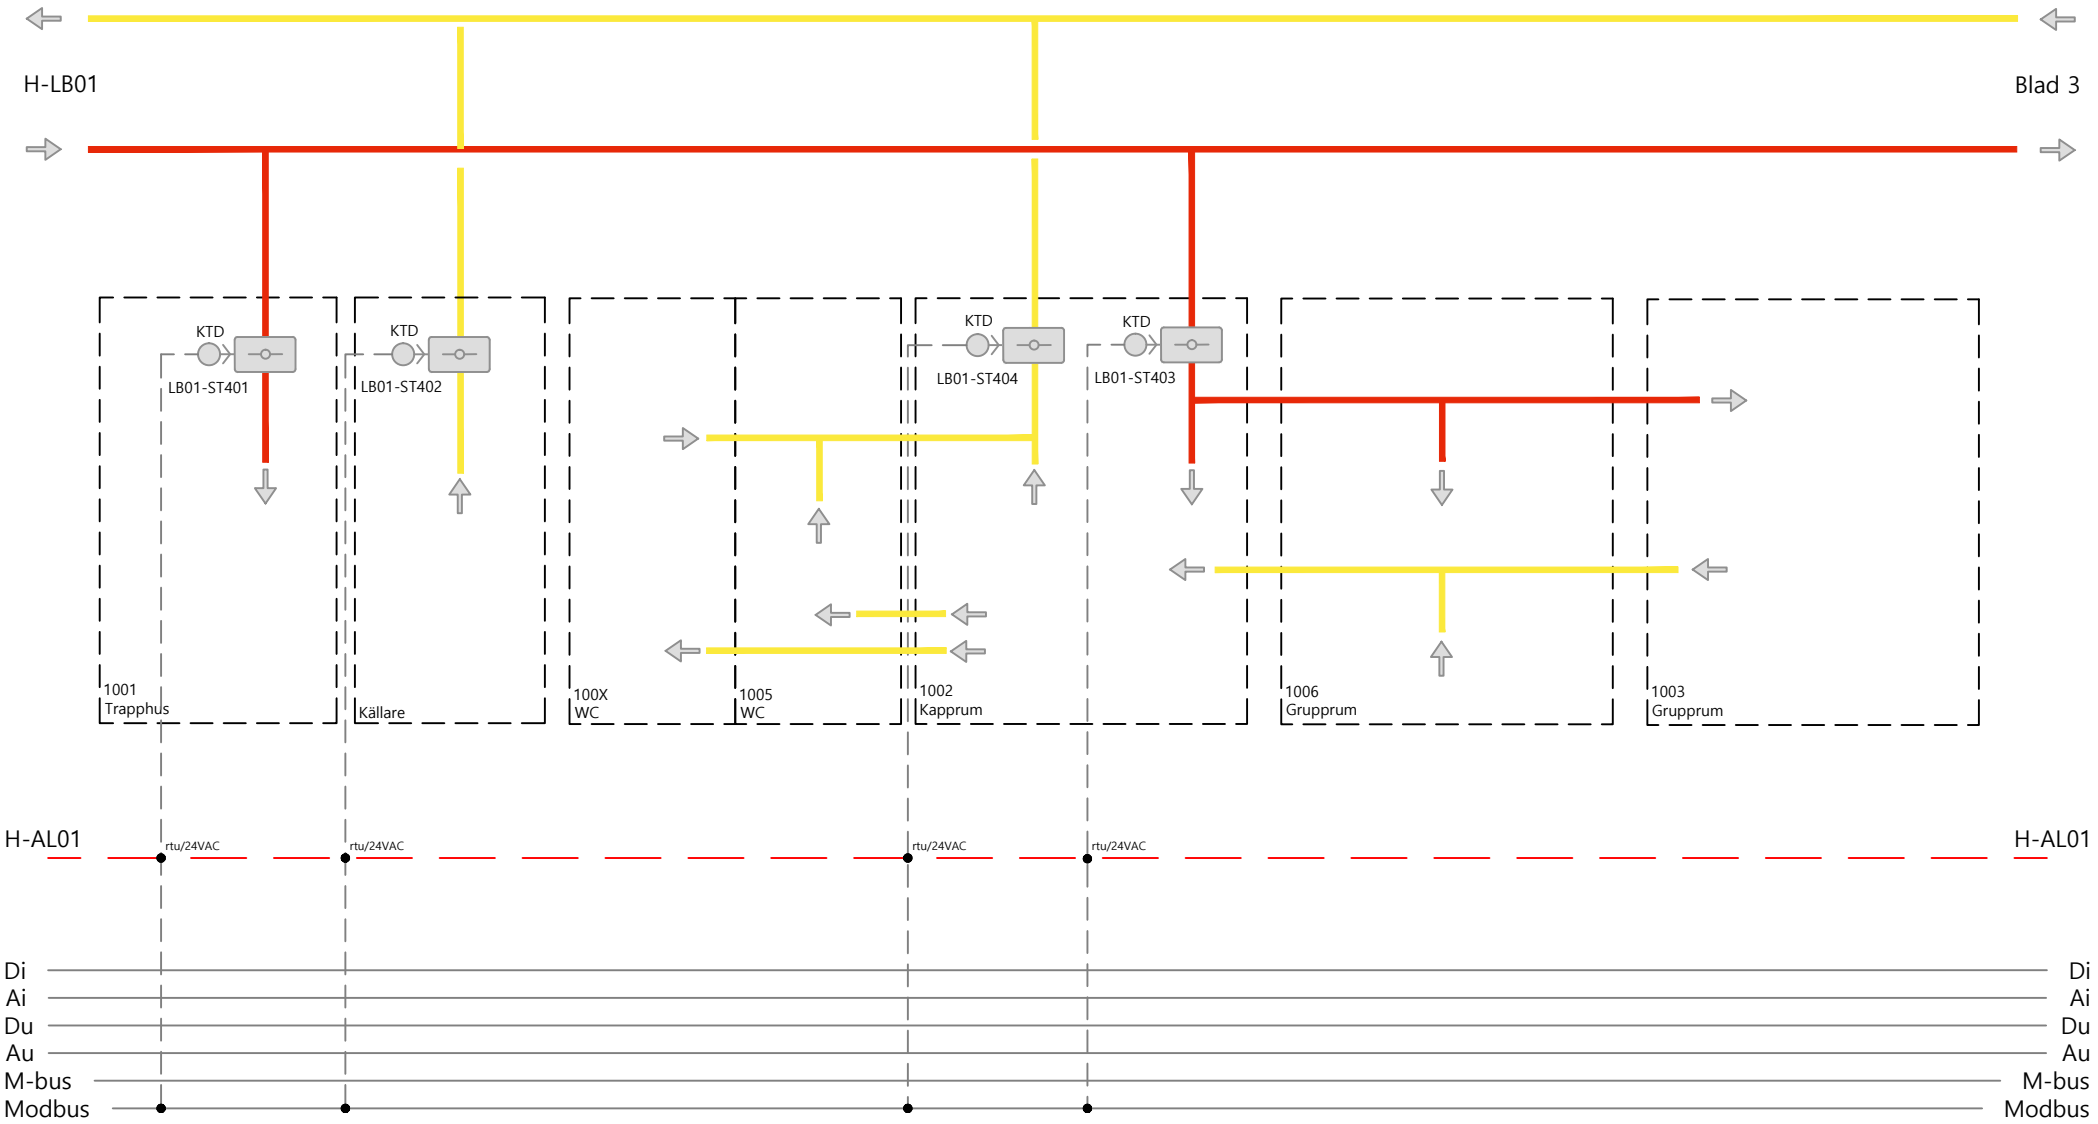
H-LB01
Blad 3
KTD
LB01-ST401
KTD
LB01-ST402
KTD
LB01-ST404
KTD
LB01-ST403
1001
Trapphus
Källare
100X
WC
1005
WC
1002
Kapprum
1006
Grupprum
1003
Grupprum
H-AL01
rtu/24VAC
rtu/24VAC
rtu/24VAC
rtu/24VAC
H-AL01
Di
Ai
Du
Au
M-bus
Modbus
Di
Ai
Du
Au
M-bus
Modbus