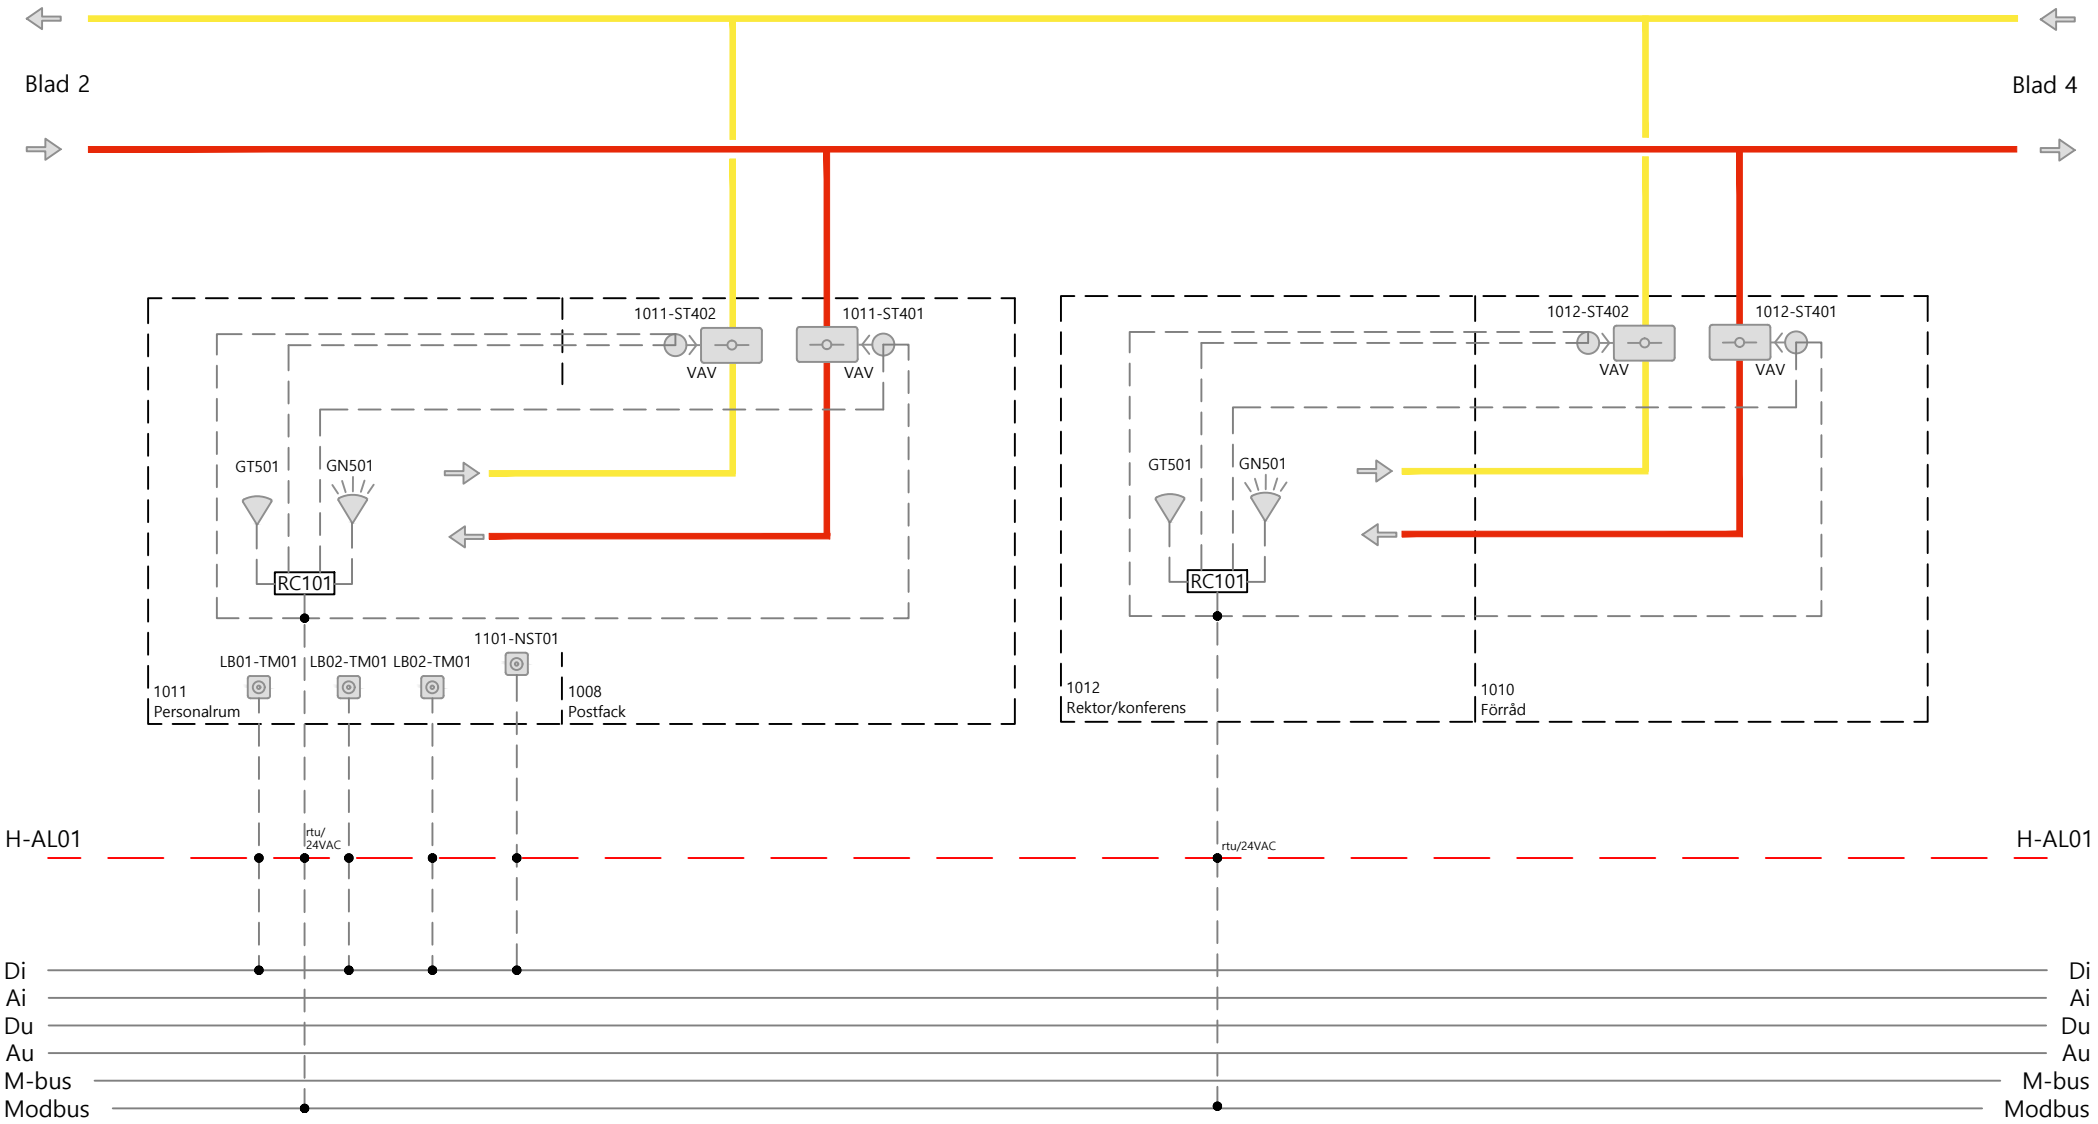
Hus H plan 10


Blad 2
Blad 4
1011-ST402
VAV
1011-ST401
VAV
GT501
GN501
RC101
1101-NST01
LB01-TM01
LB02-TM01
LB02-TM01
1011
Personalrum
1008
Postfack
1012-ST402
VAV
1012-ST401
VAV
GT501
GN501
RC101
1012
Rektor/konferens
1010
Förråd
H-AL01
rtu/
24VAC
rtu/24VAC
H-AL01
Di
Ai
Du
Au
M-bus
Modbus
Di
Ai
Du
Au
M-bus
Modbus