Hus H plan 10

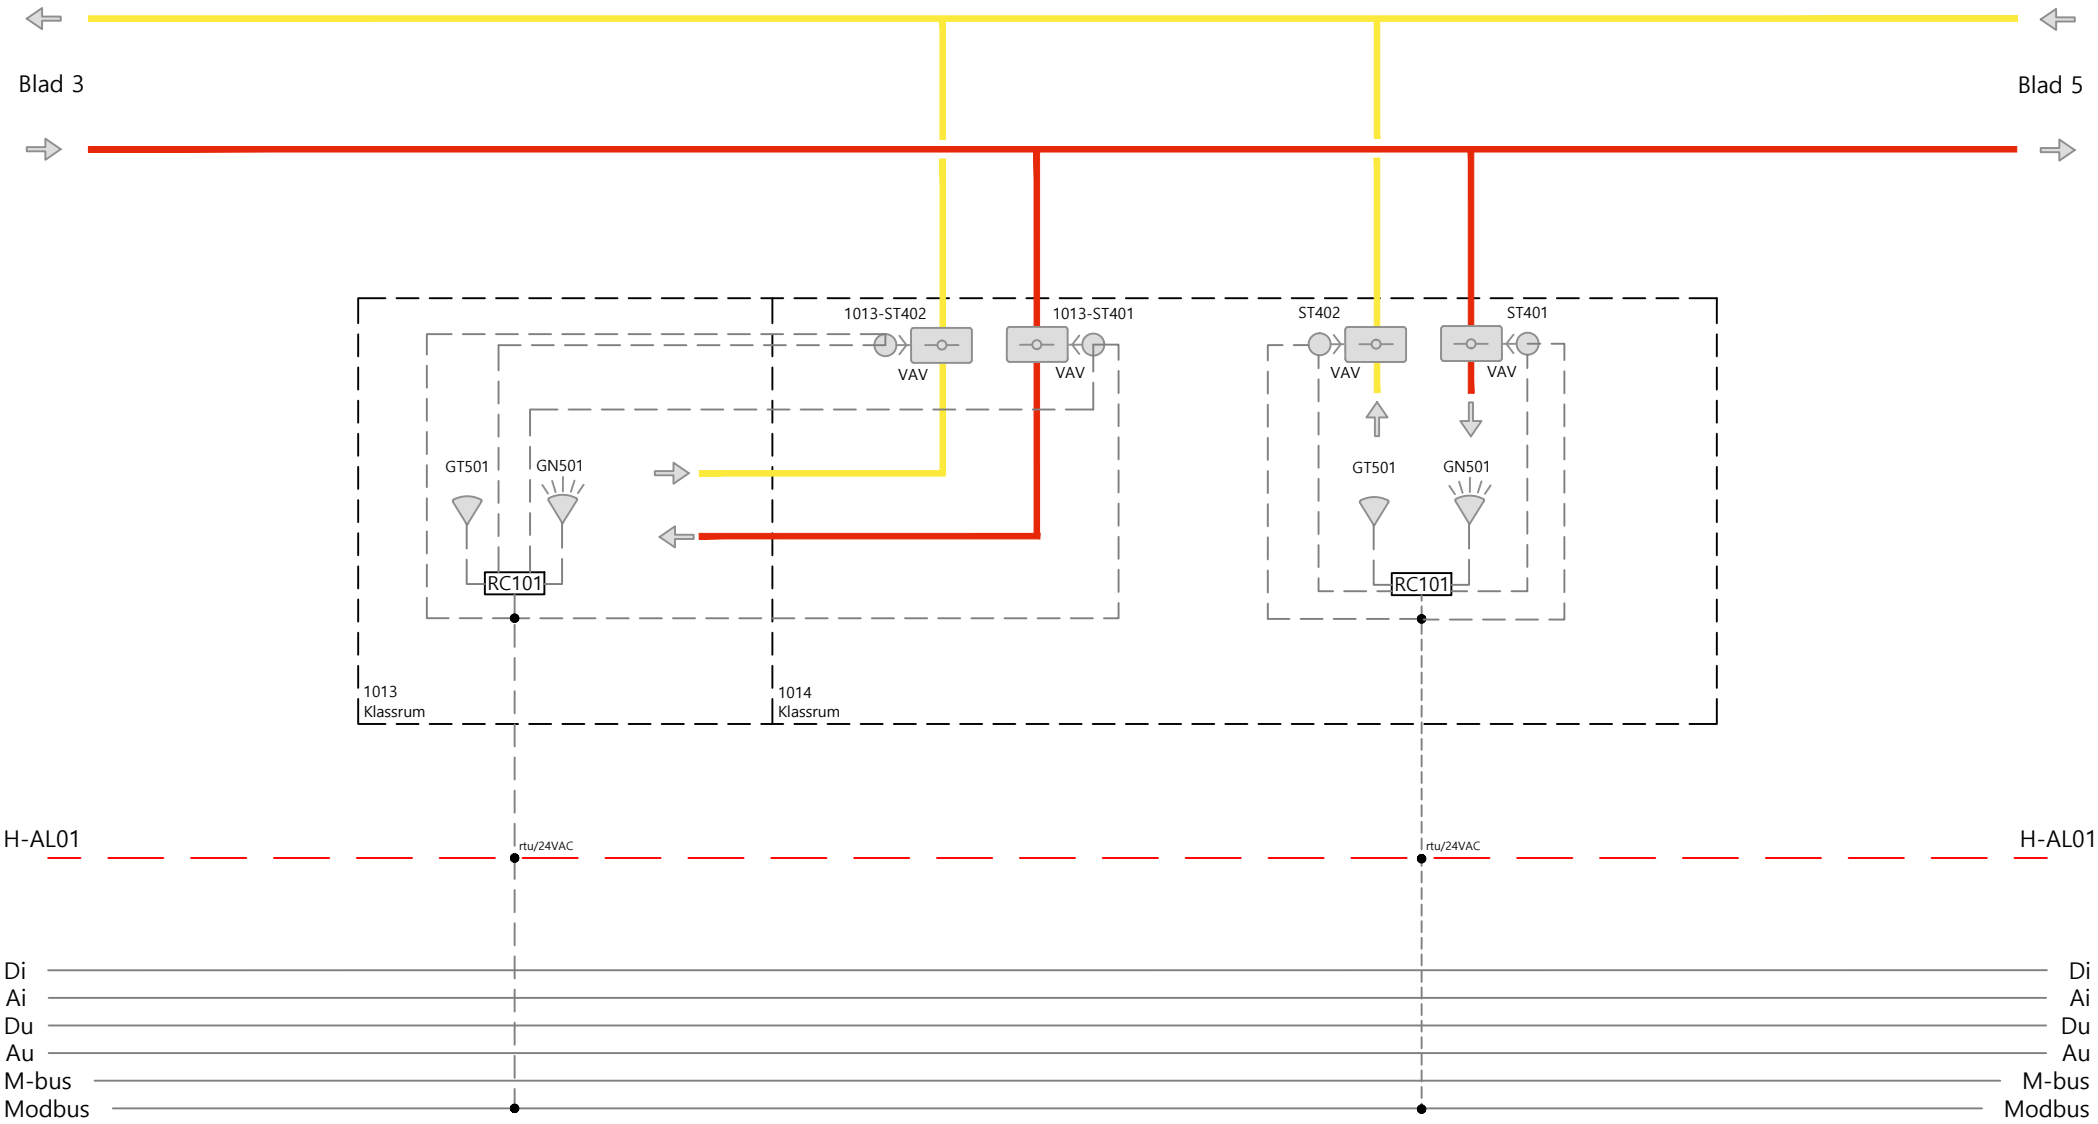
Blad 3
Blad 5
1013-ST402
1013-ST401
ST402
ST401
VAV
VAV
VAV
VAV
GT501
GN501
GT501
GN501
RC101
RC101
1013
Klassrum
1014
Klassrum
H-AL01
H-AL01
rtu/24VAC
rtu/24VAC
Di
Ai
Du
Au
M-bus
Modbus
Di
Ai
Du
Au
M-bus
Modbus