Hus H plan 11

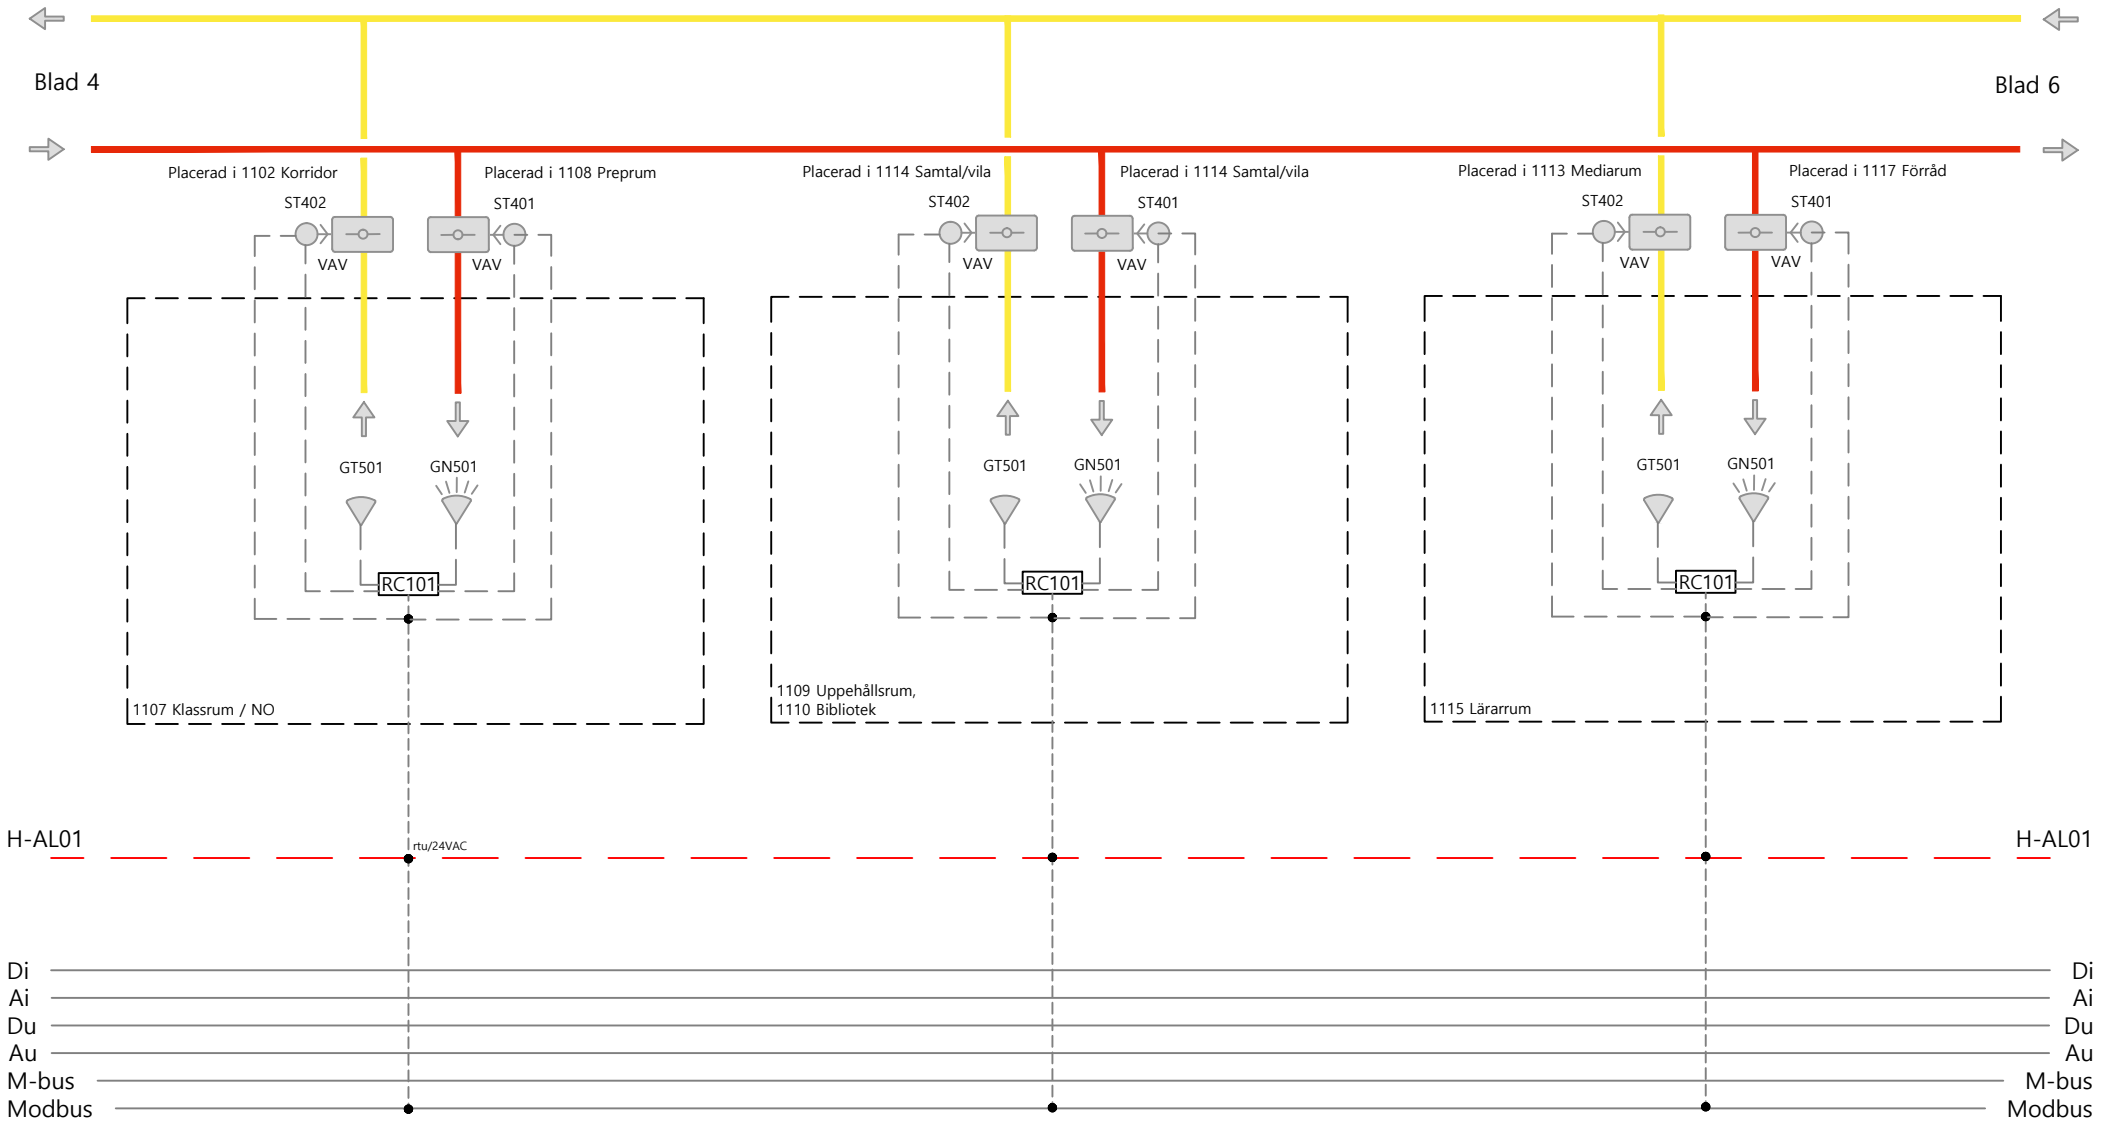
Blad 4
Blad 6
Placerad i 1102 Korridor
Placerad i 1108 Preprum
Placerad i 1114 Samtal/vila
Placerad i 1114 Samtal/vila
Placerad i 1113 Mediarum
Placerad i 1117 Förråd
ST402
ST401
VAV
GT501
GN501
RC101
1107 Klassrum / NO
1109 Uppehållsrum,
1110 Bibliotek
1115 Lärarrum
H-AL01
rtu/24VAC
Di
Ai
Du
Au
M-bus
Modbus