Hus H plan 11

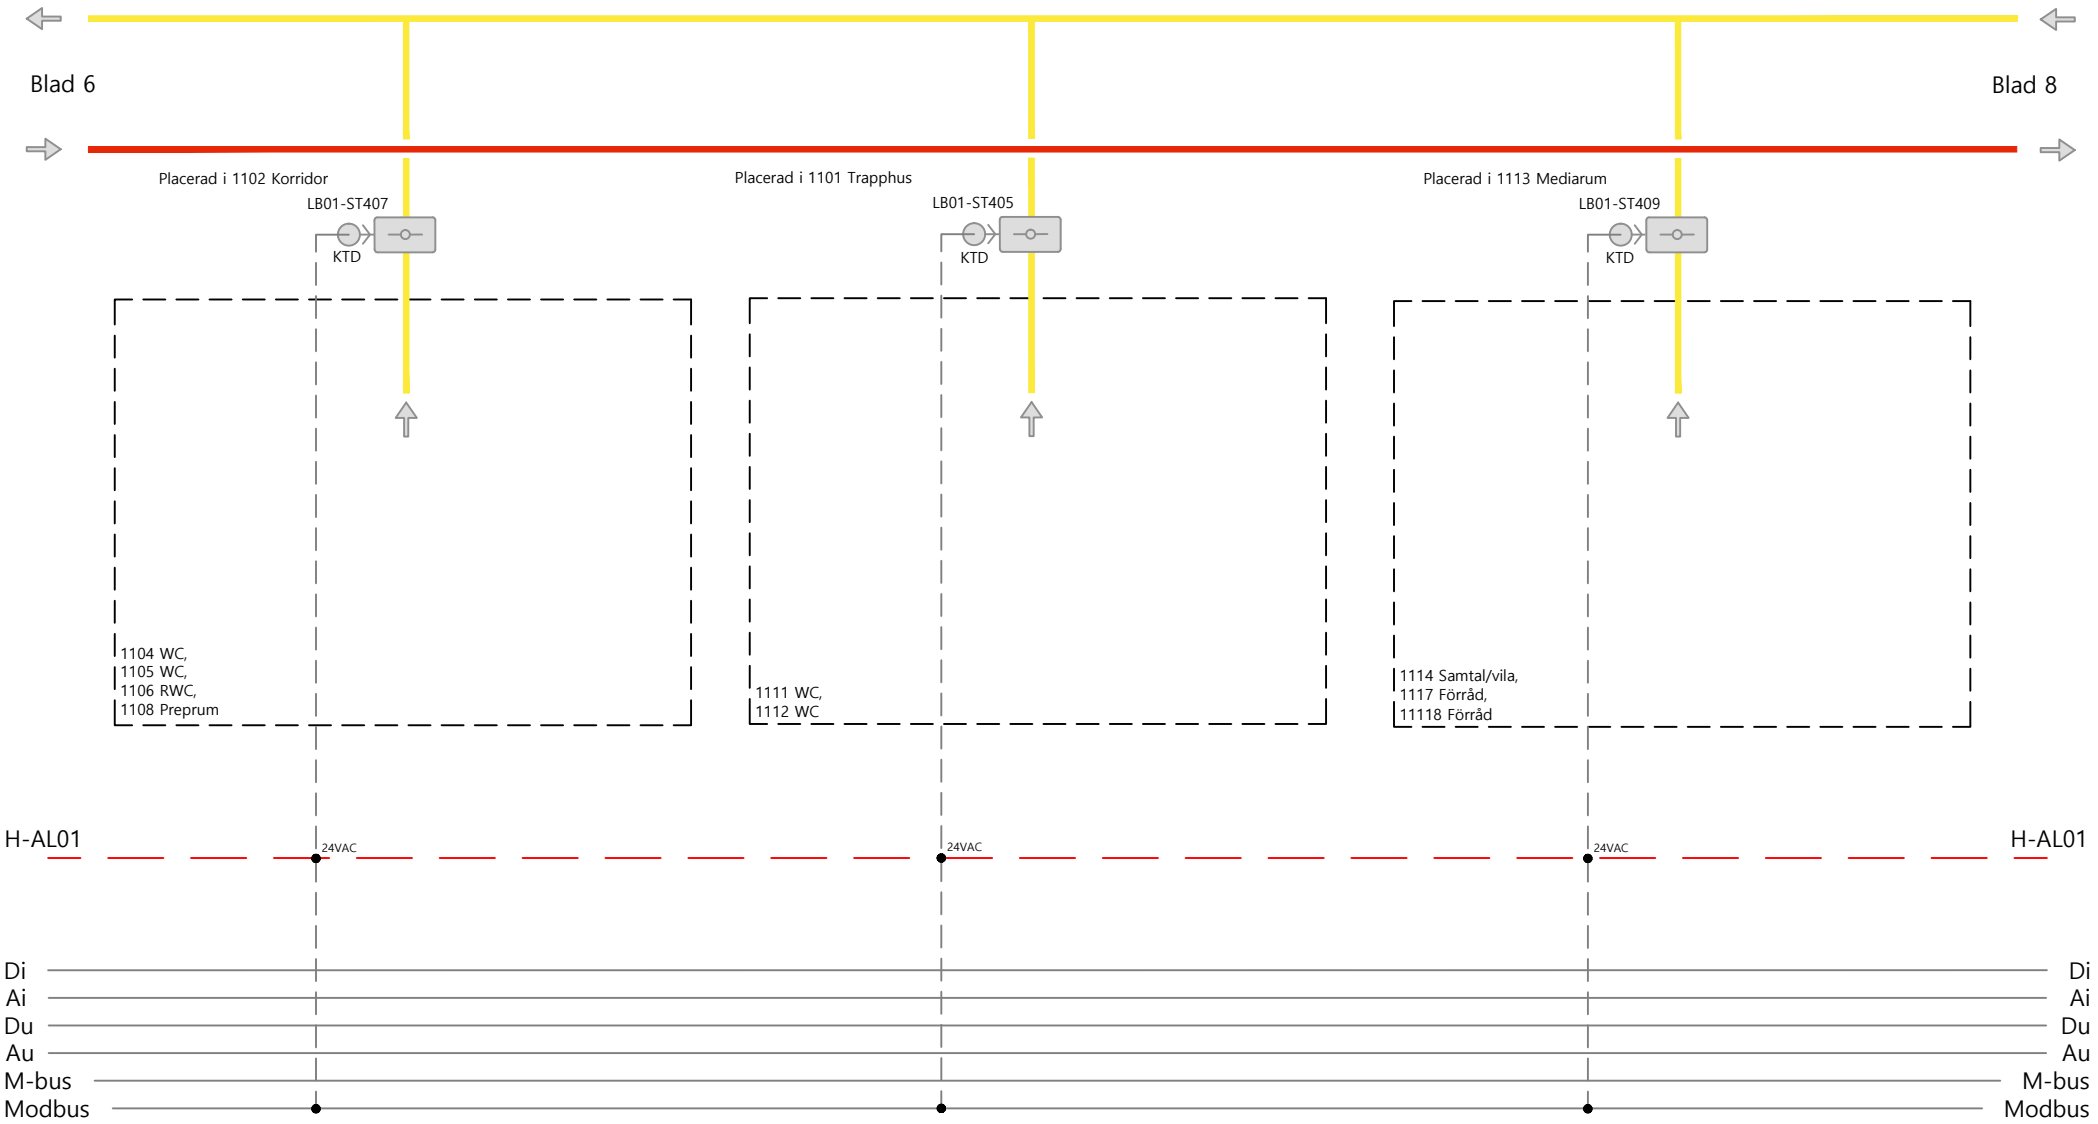
Blad 6
Blad 8
Placerad i 1102 Korridor
LB01-ST407
KTD
Placerad i 1101 Trapphus
LB01-ST405
KTD
Placerad i 1113 Mediarum
LB01-ST409
KTD
1104 WC,
1105 WC,
1106 RWC,
1108 Preprum
1111 WC,
1112 WC
1114 Samtal/vila,
1117 Förråd,
11118 Förråd
H-AL01
24VAC
24VAC
24VAC
H-AL01
Di
Ai
Du
Au
M-bus
Modbus
Di
Ai
Du
Au
M-bus
Modbus