Hus H plan 11

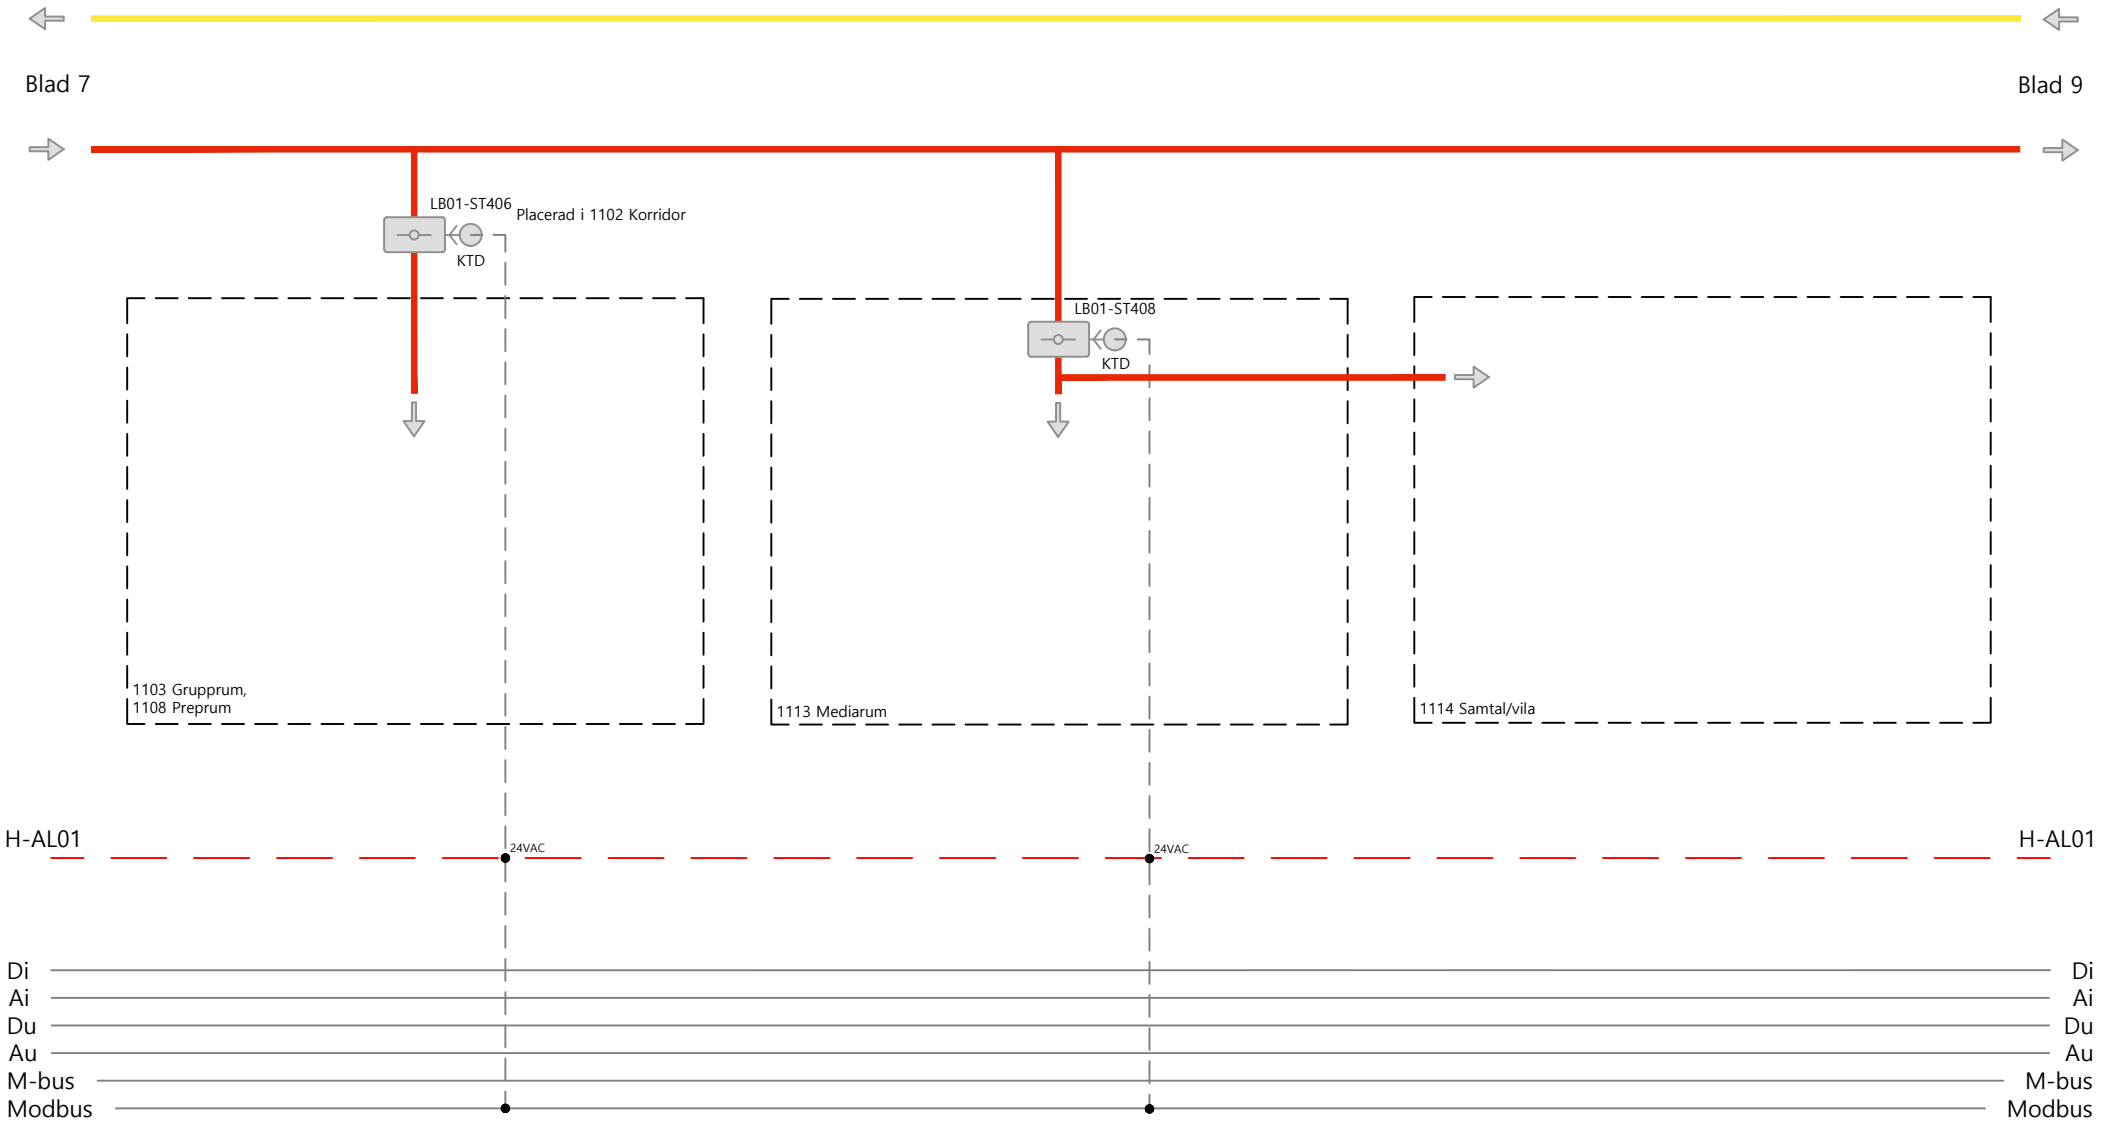
Blad 7
Blad 9
LB01-ST406
Placerad i 1102 Korridor
KTD
LB01-ST408
KTD
1103 Grupprum,
1108 Preprum
1113 Mediarum
1114 Samtal/vila
H-AL01
24VAC
24VAC
H-AL01
Di
Ai
Du
Au
M-bus
Modbus
Di
Ai
Du
Au
M-bus
Modbus