Hus H Plan 10

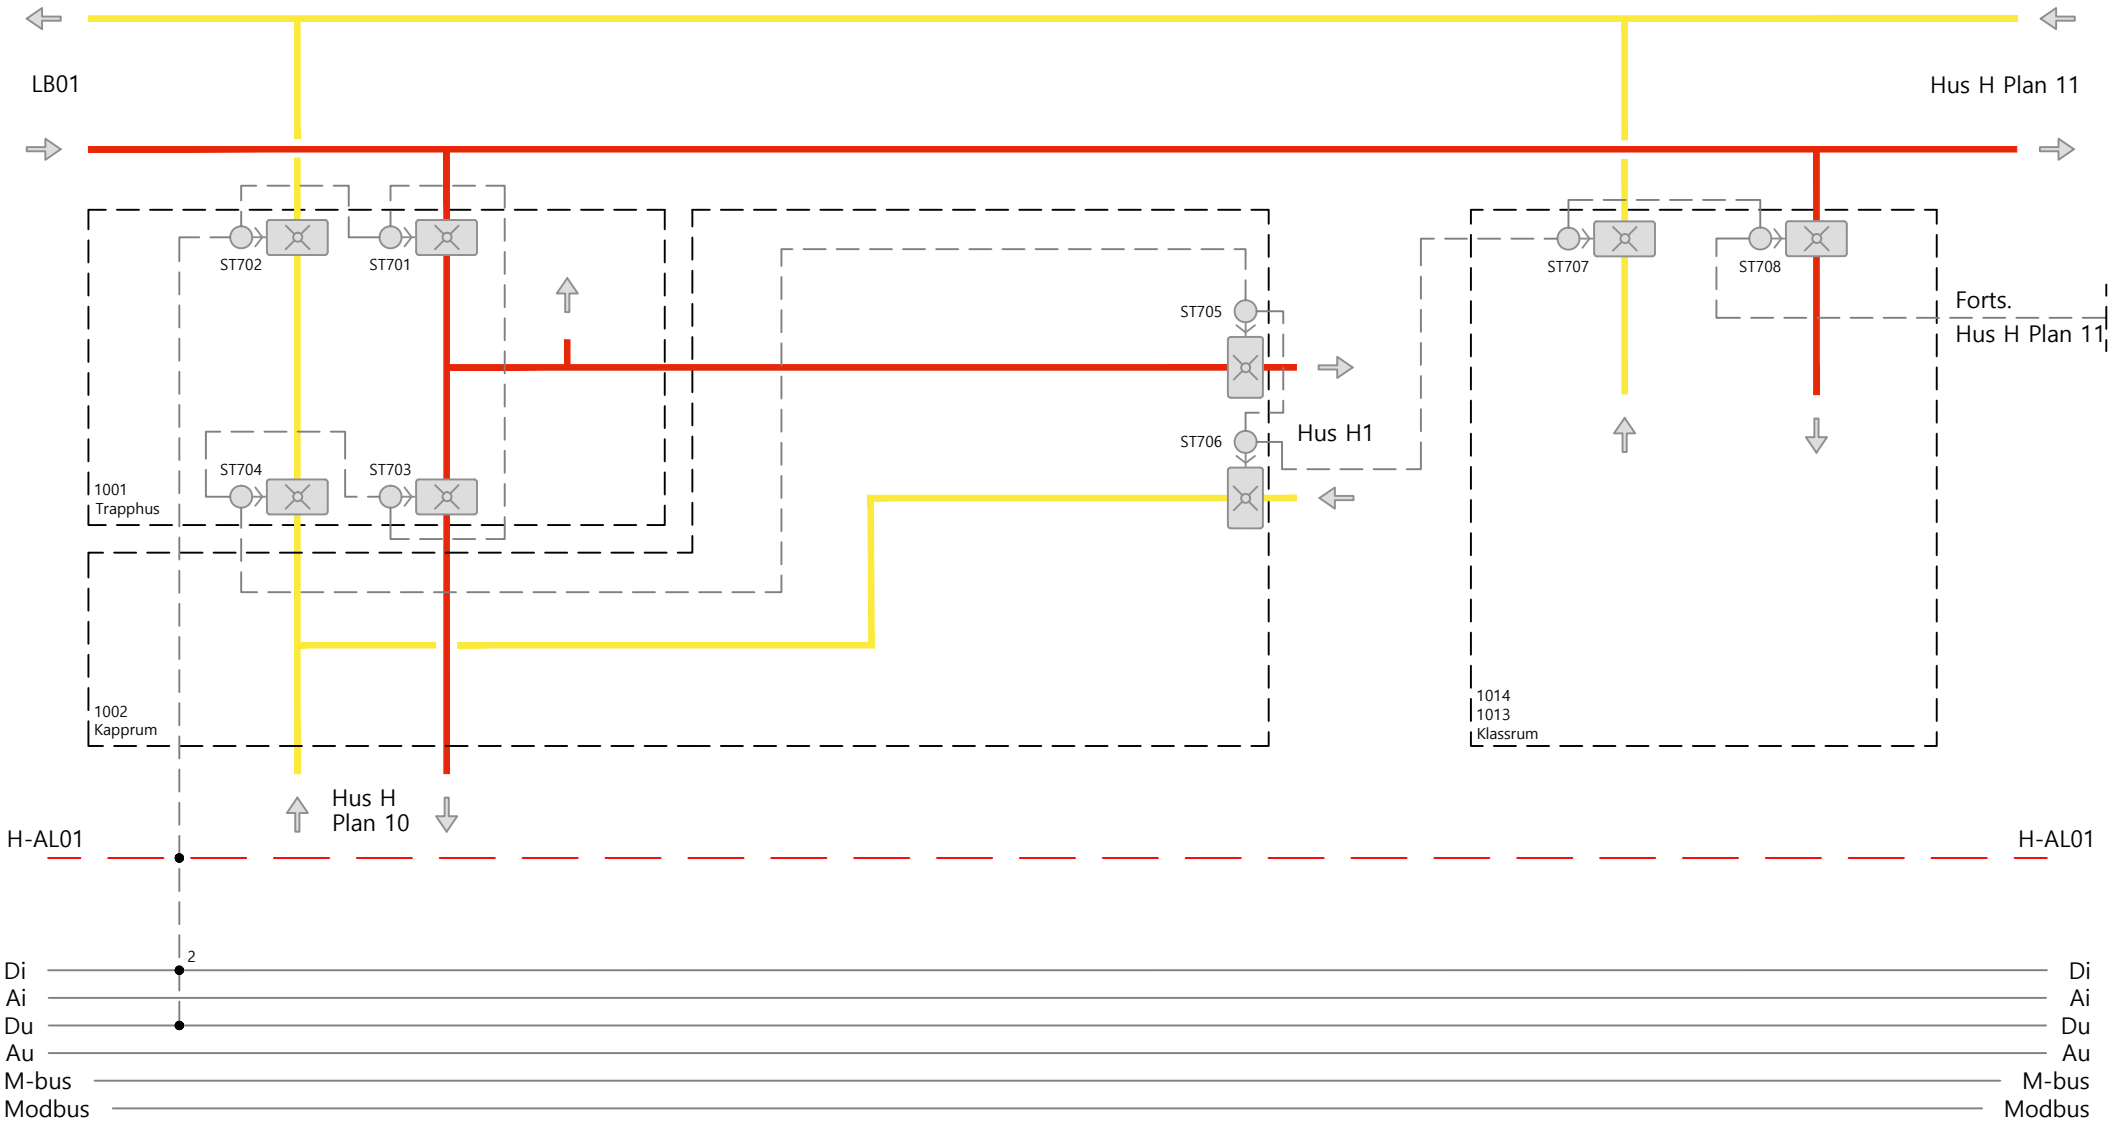
LB01
Hus H Plan 11
ST702
ST701
ST705
ST707
ST708
Forts.
Hus H Plan 11
ST706
Hus H1
ST704
ST703
1001
Trapphus
1002
Kapprum
1014
1013
Klassrum
Hus H
Plan 10
H-AL01
H-AL01
2
Di
Ai
Du
Au
M-bus
Modbus
Di
Ai
Du
Au
M-bus
Modbus