Hus H3

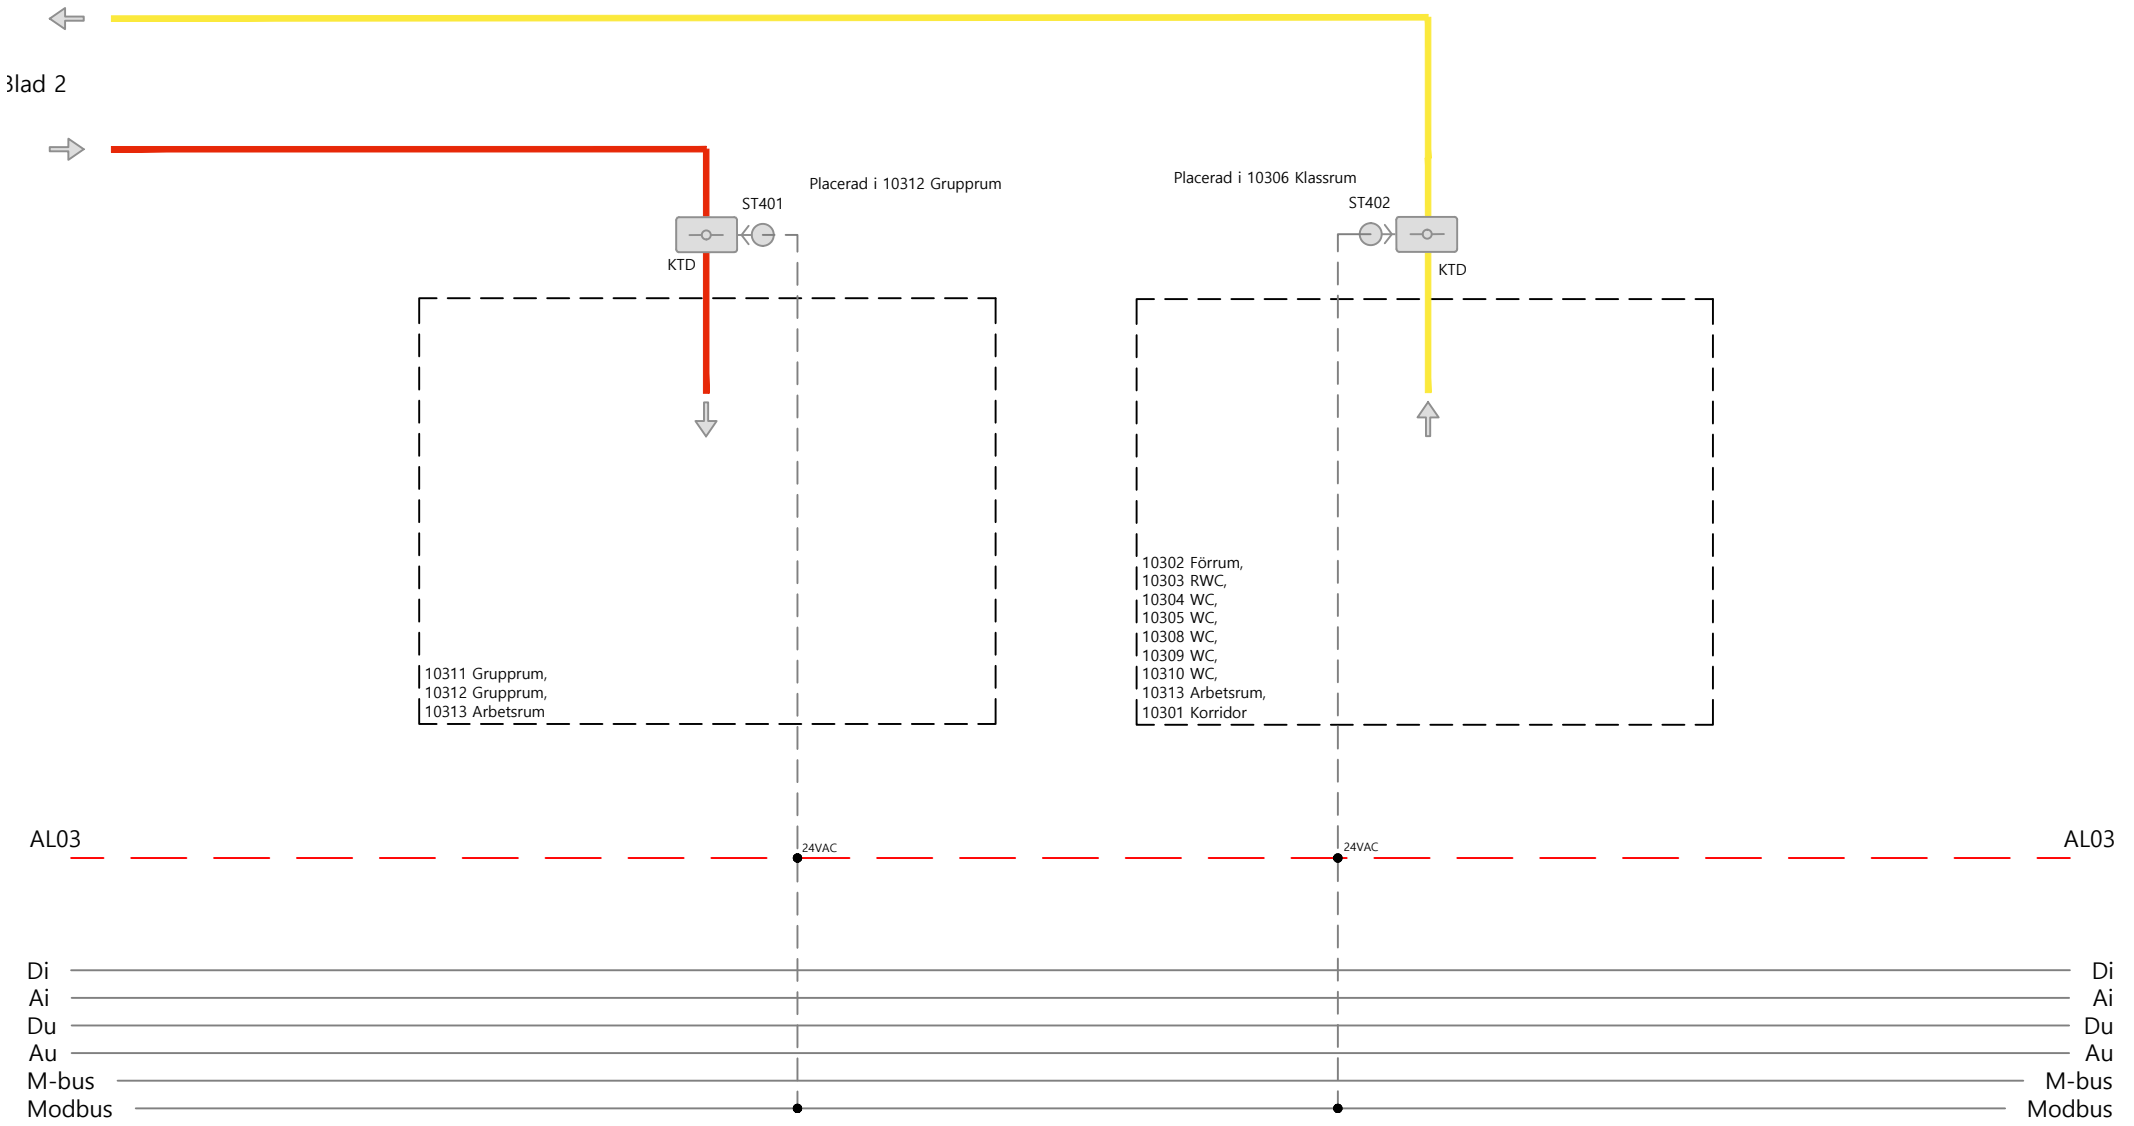
Blad 2
Placerad i 10312 Grupprum
ST401
KTD
Placerad i 10306 Klassrum
ST402
KTD
10311 Grupprum,
10312 Grupprum,
10313 Arbetsrum
10302 Förrum,
10303 RWC,
10304 WC,
10305 WC,
10308 WC,
10309 WC,
10310 WC,
10313 Arbetsrum,
10301 Korridor
AL03
24VAC
24VAC
AL03
Di
Ai
Du
Au
M-bus
Modbus
Di
Ai
Du
Au
M-bus
Modbus