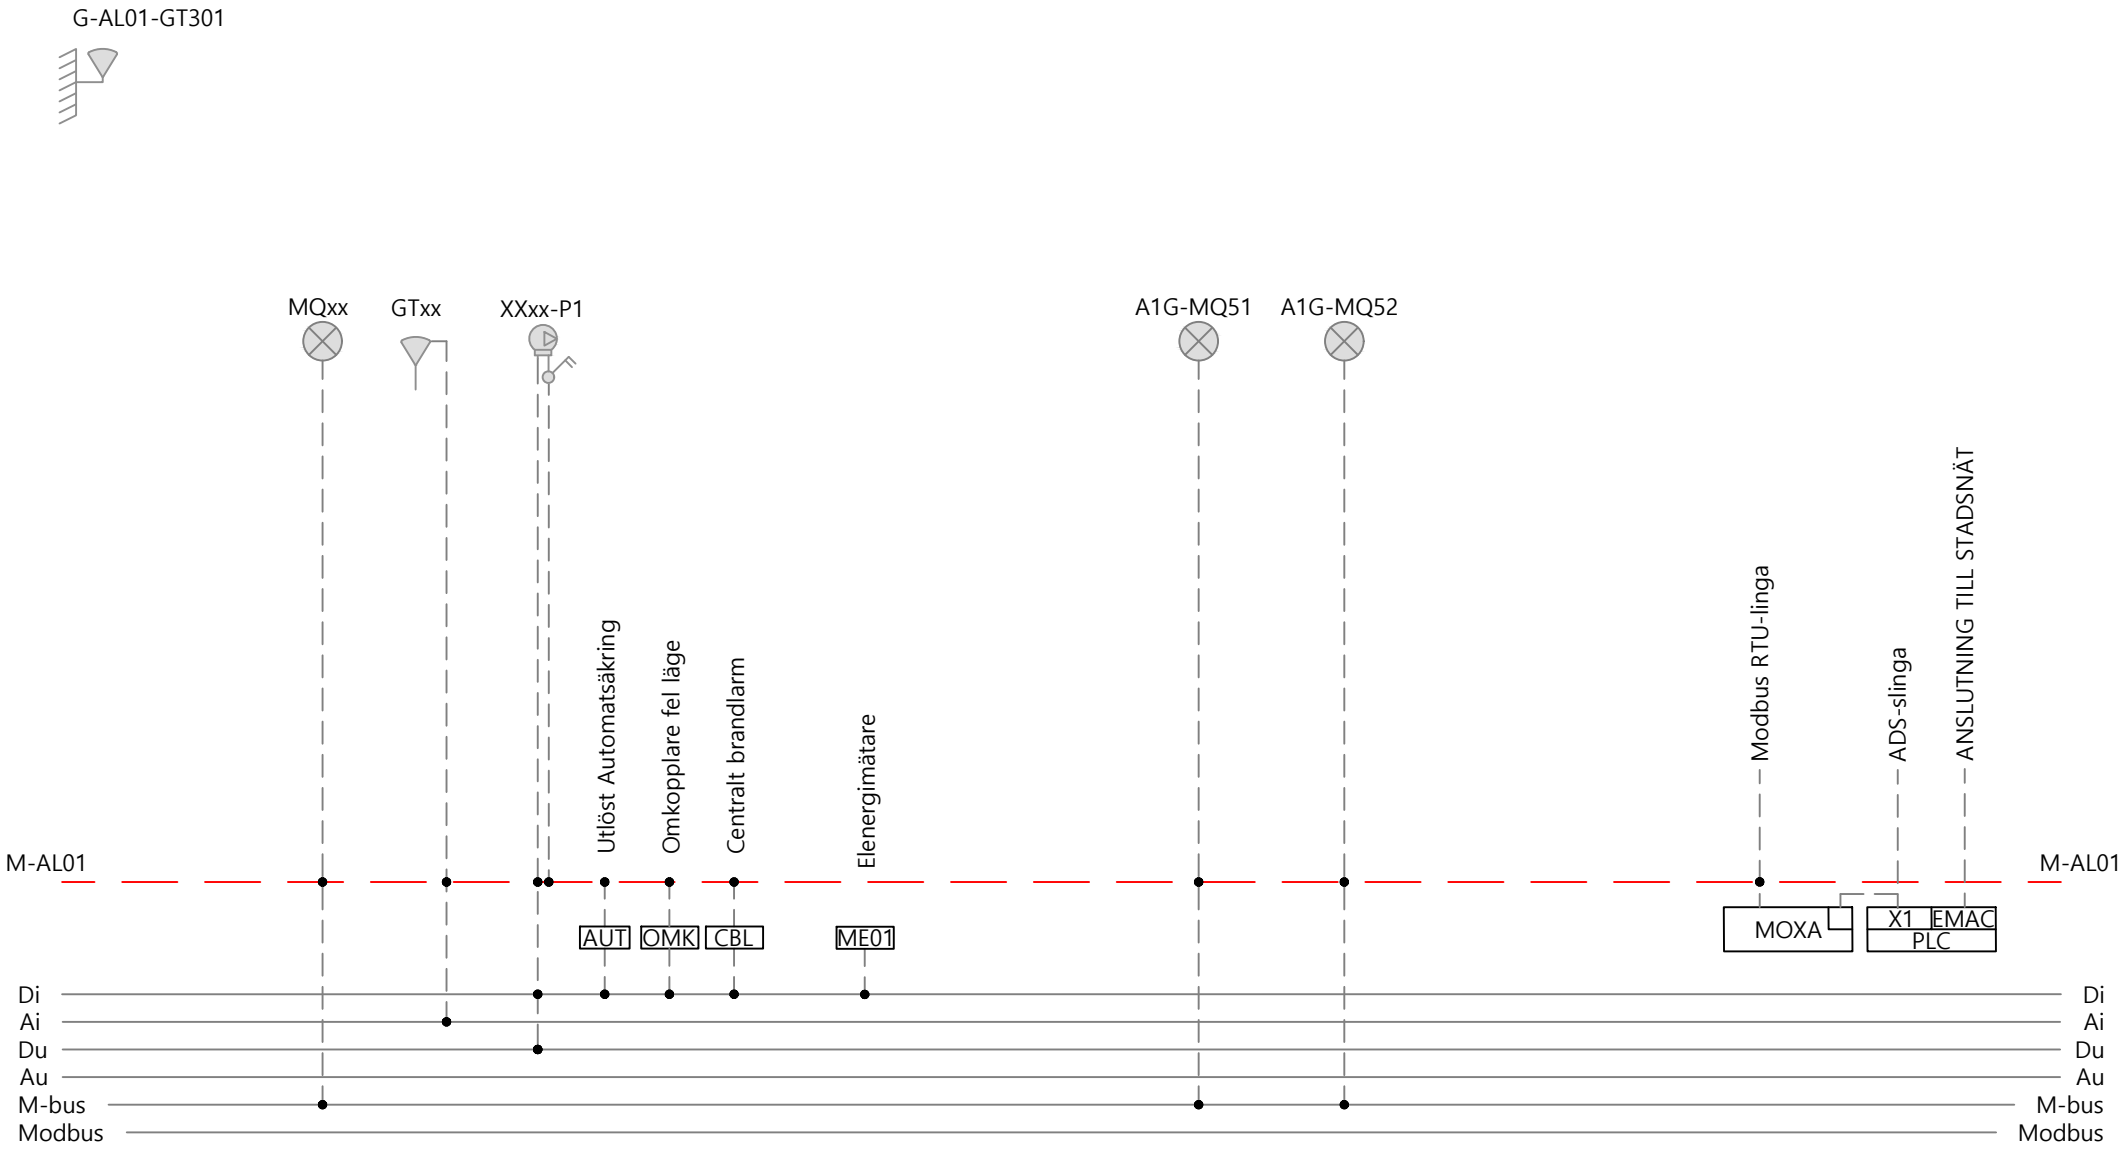
G-AL01-GT301
MQxx
GTxx
XXxx-P1
A1G-MQ51
A1G-MQ52
Utlöst Automatsäkring
Omkopplare fel läge
Centralt brandlarm
Elenergimätare
Modbus RTU-linga
ADS-slinga
ANSLUTNING TILL STADSNÄT
M-AL01
M-AL01
AUT
OMK
CBL
ME01
MOXA
X1
EMAC
PLC
Di
Ai
Du
Au
M-bus
Modbus
Di
Ai
Du
Au
M-bus
Modbus