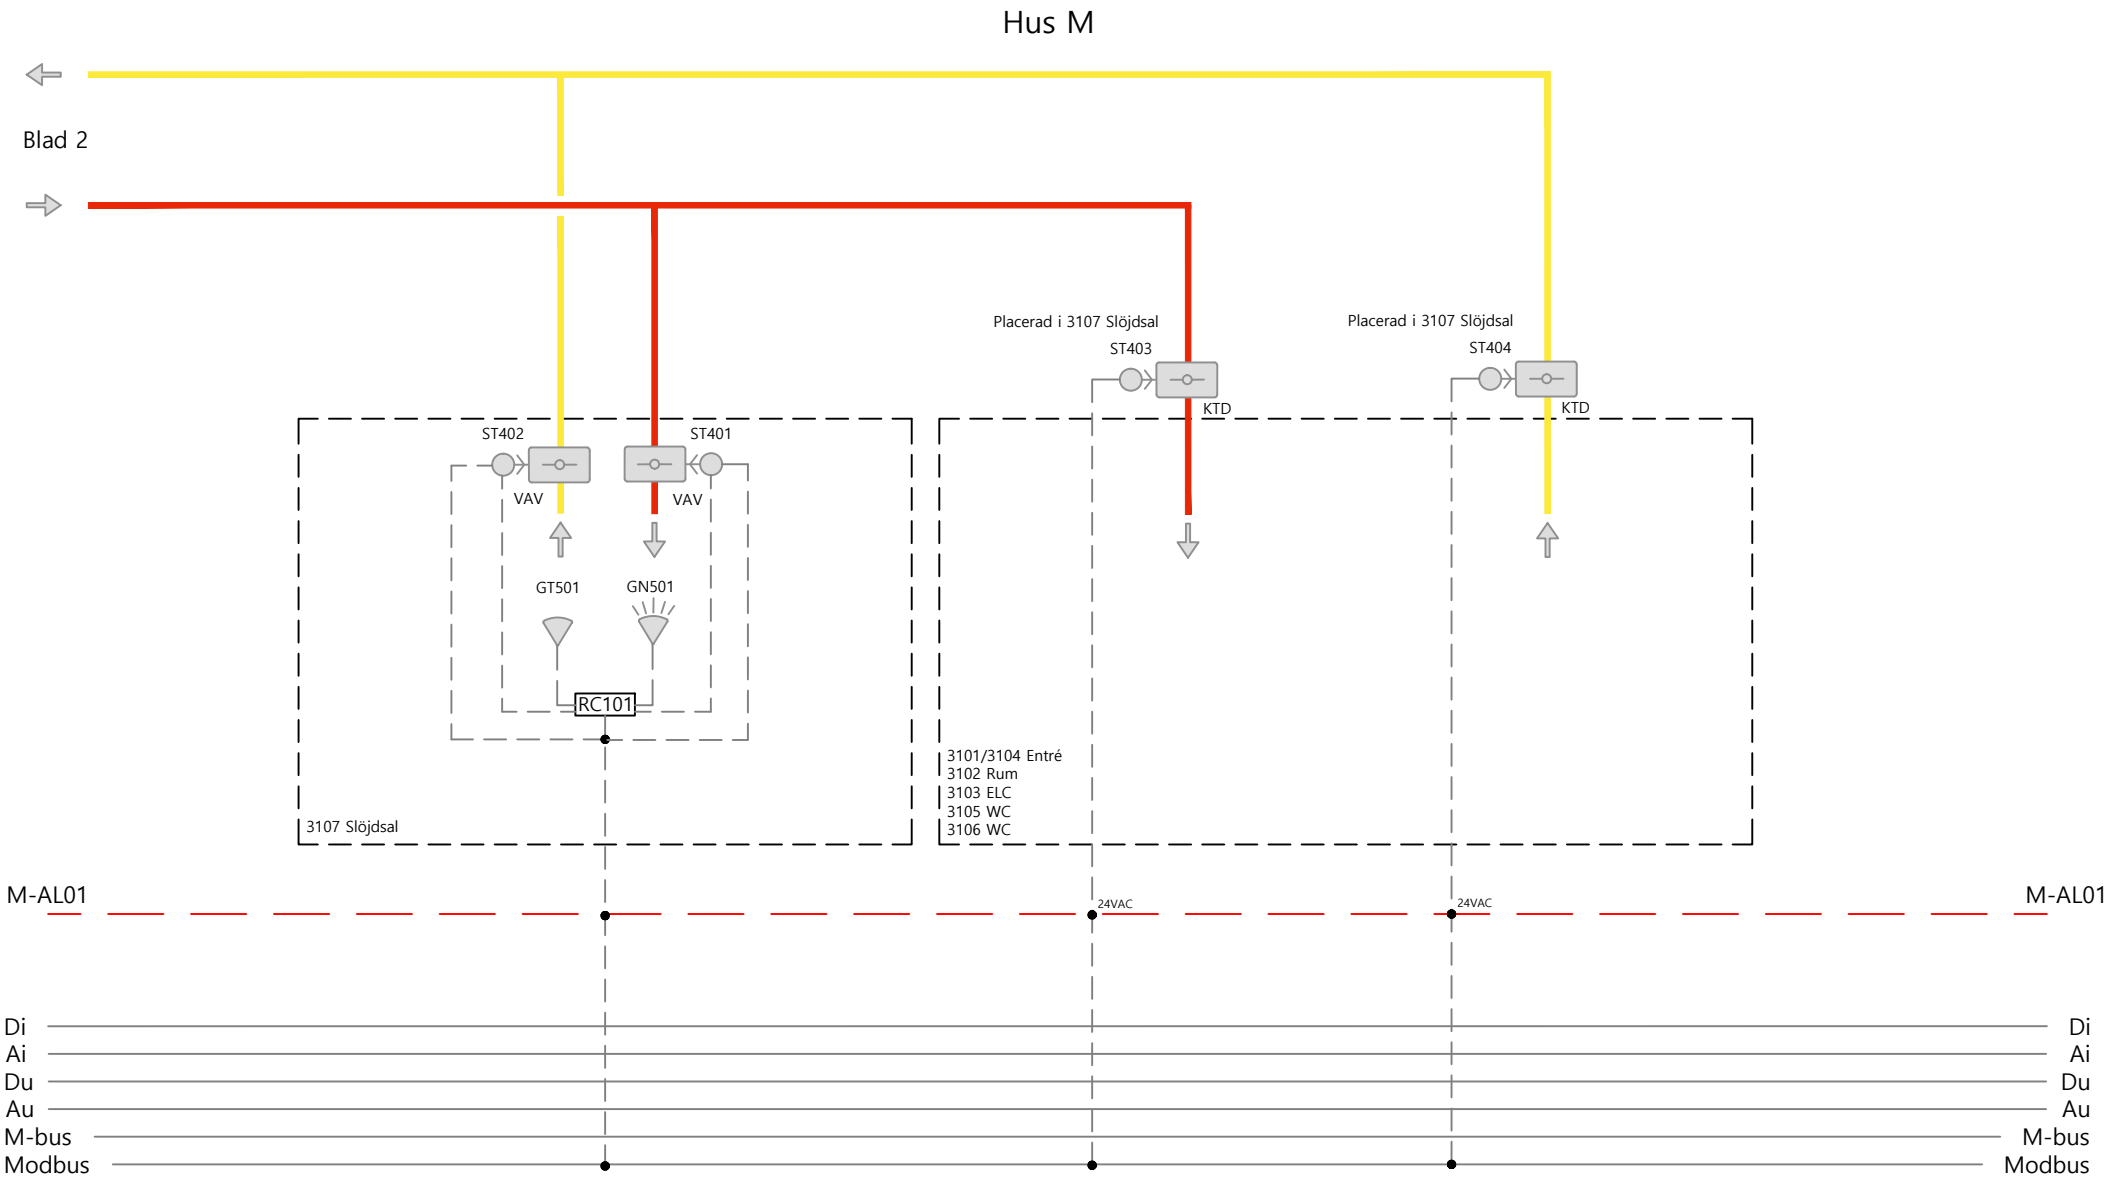
Hus M
Blad 2
Placerad i 3107 Slöjdsal
ST403
KTD
Placerad i 3107 Slöjdsal
ST404
KTD
ST402
VAV
ST401
VAV
GT501
GN501
RC101
3107 Slöjdsal
3101/3104 Entré
3102 Rum
3103 ELC
3105 WC
3106 WC
M-AL01
24VAC
24VAC
M-AL01
Di
Ai
Du
Au
M-bus
Modbus
Di
Ai
Du
Au
M-bus
Modbus