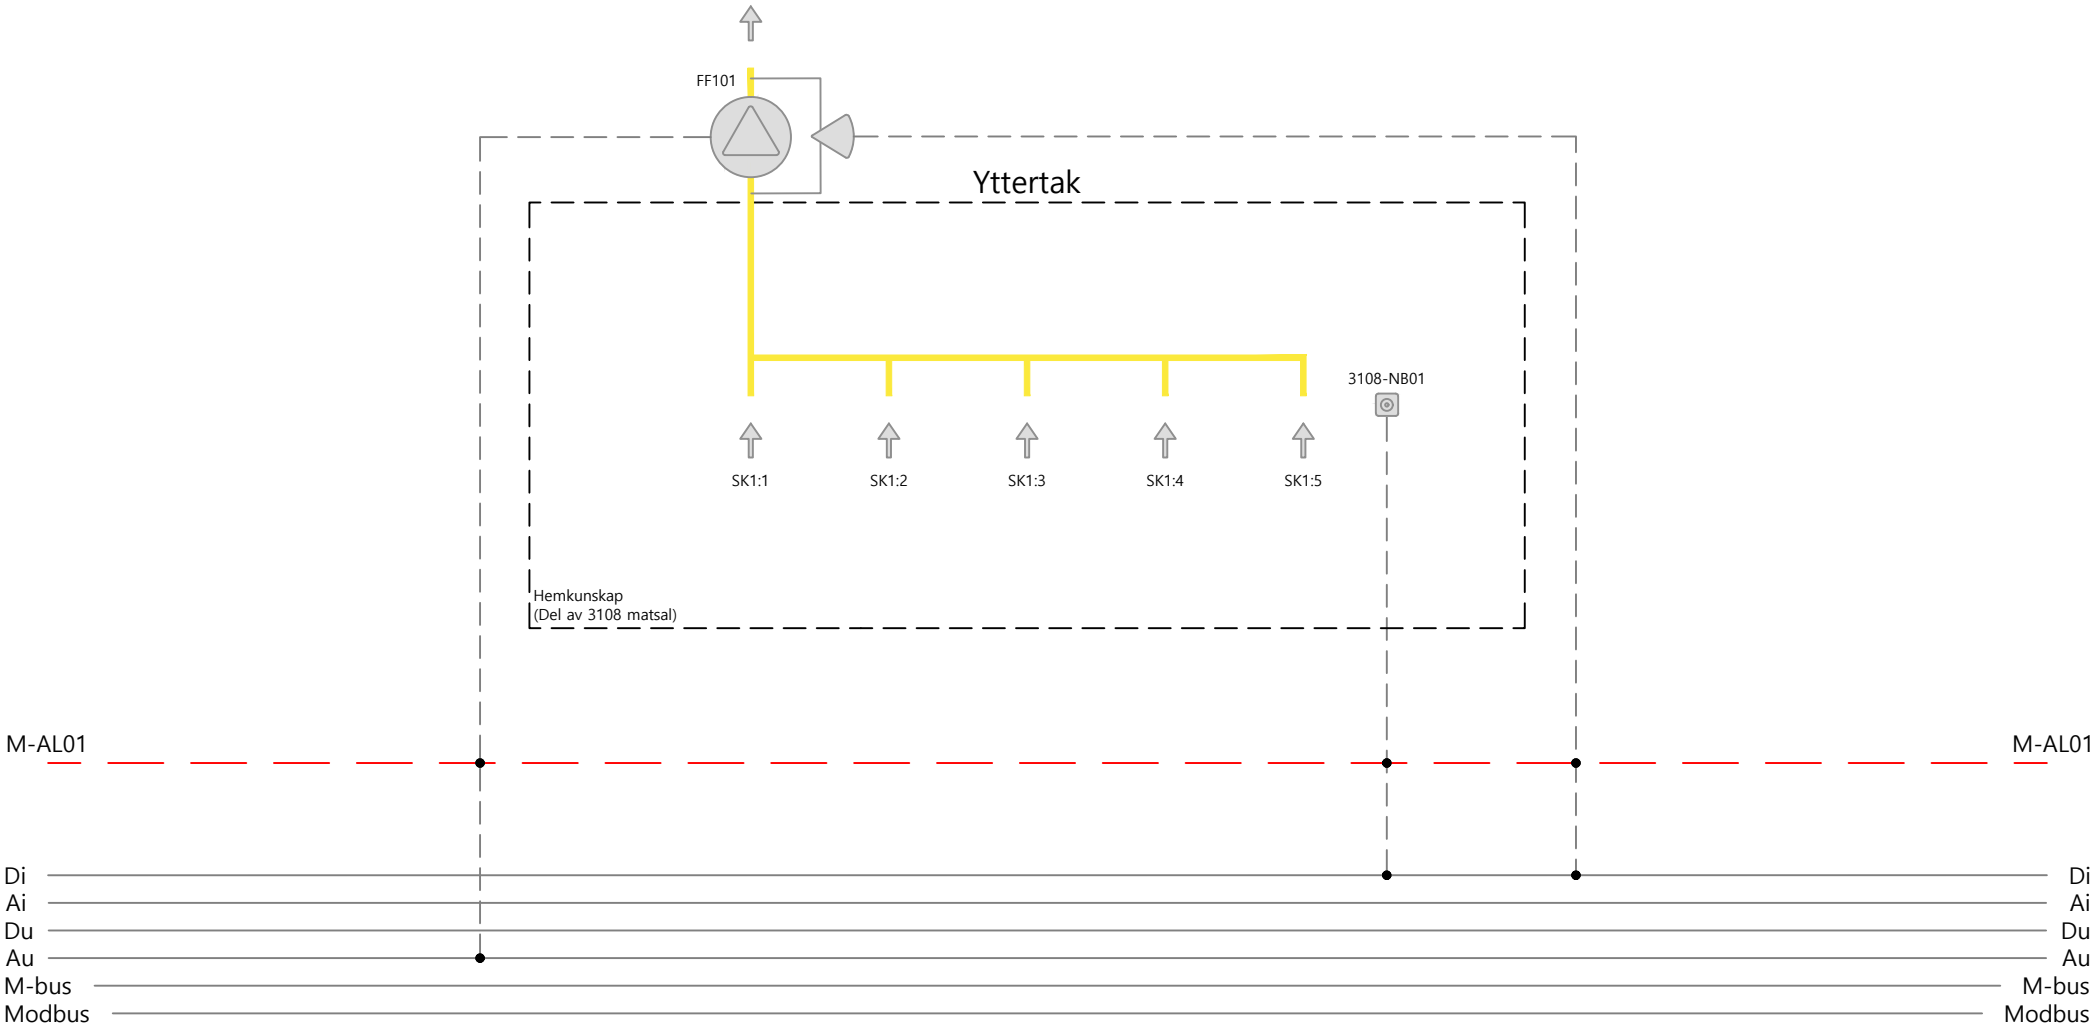
FF101
Yttertak
3108-NB01
SK1:1
SK1:2
SK1:3
SK1:4
SK1:5
Hemkunskap
(Del av 3108 matsal)
M-AL01
M-AL01
Di
Ai
Du
Au
M-bus
Modbus
Di
Ai
Du
Au
M-bus
Modbus