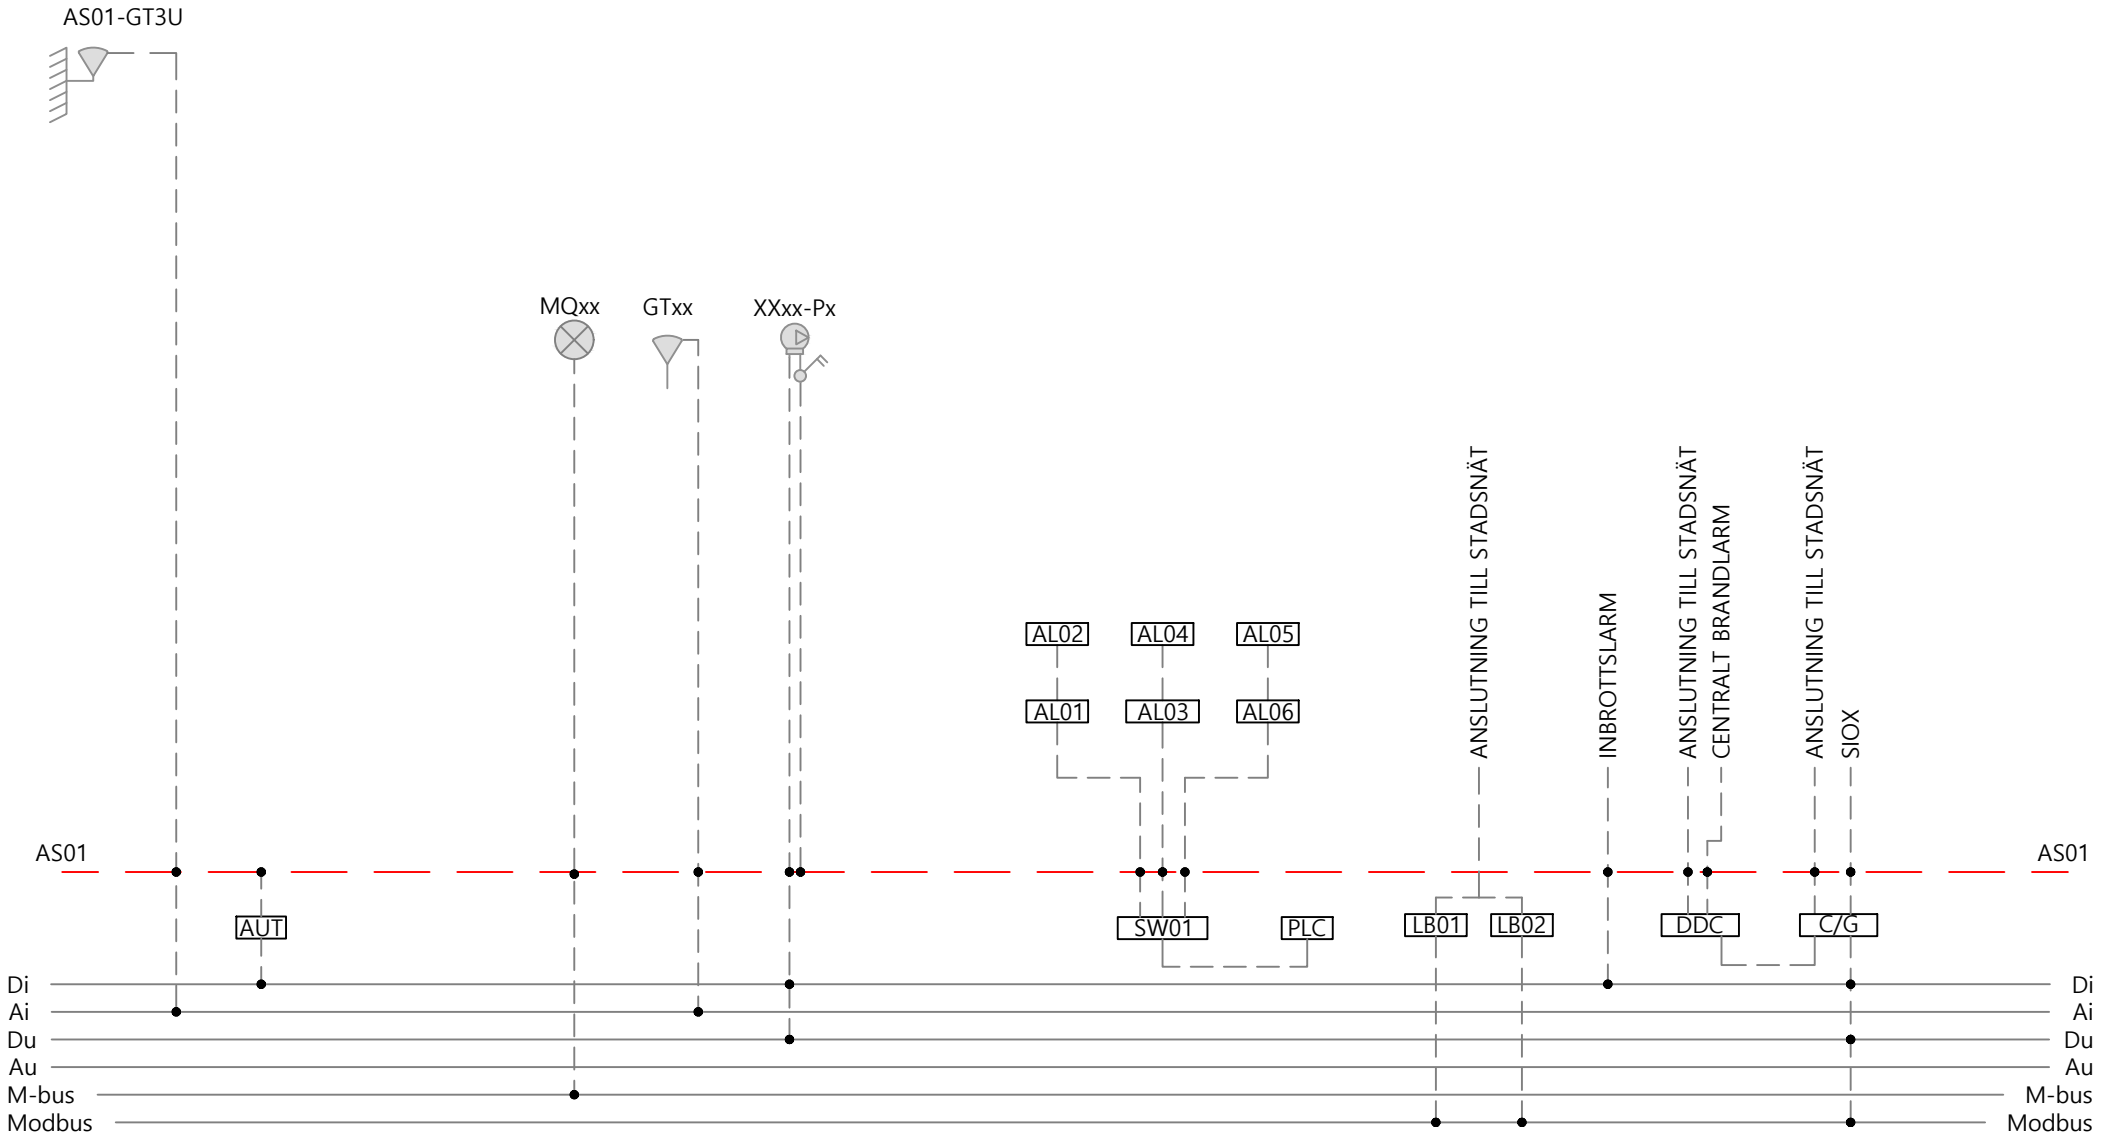
AS01-GT3U
MQxx
GTxx
XXxx-Px
AL02
AL04
AL05
AL01
AL03
AL06
ANSLUTNING TILL STADSNÄT
INBROTTSLARM
ANSLUTNING TILL STADSNÄT
CENTRALT BRANDLARM
ANSLUTNING TILL STADSNÄT
SIOX
AS01
AS01
AUT
SW01
PLC
LB01
LB02
DDC
C/G
Di
Ai
Du
Au
M-bus
Modbus
Di
Ai
Du
Au
M-bus
Modbus