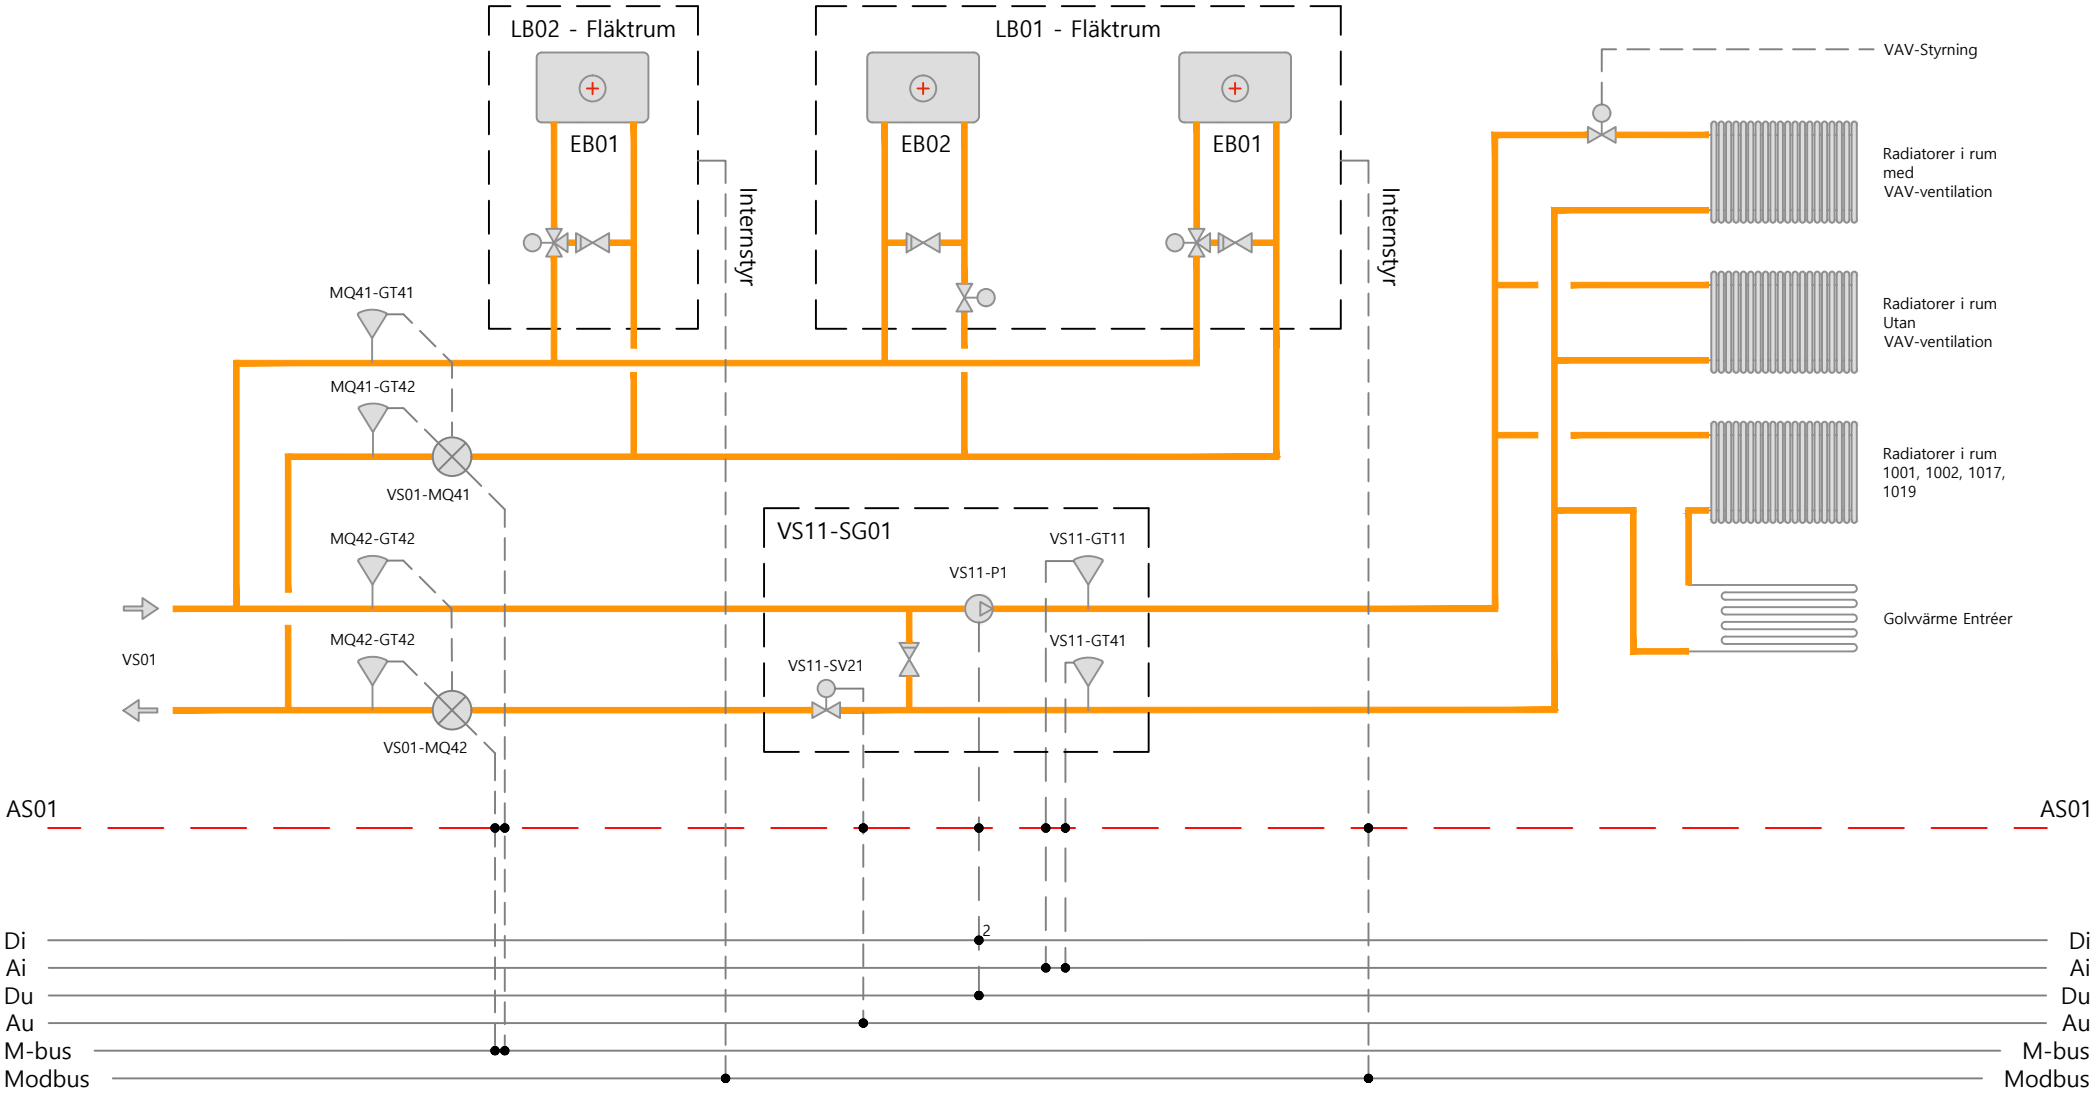

LB02 - Fläktrum
EB01
LB01 - Fläktrum
EB02
EB01
Internstyr
Internstyr
VAV-Styrning
Radiatorer i rum
med
VAV-ventilation
Radiatorer i rum
Utan
VAV-ventilation
Radiatorer i rum
1001, 1002, 1017,
1019
Golvvärme Entréer
MQ41-GT41
MQ41-GT42
VS01-MQ41
VS11-SG01
VS11-GT11
VS11-P1
MQ42-GT42
VS01
MQ42-GT42
VS11-GT41
VS11-SV21
VS01-MQ42
AS01
AS01
Di
Ai
Du
Au
M-bus
Modbus
2
Di
Ai
Du
Au
M-bus
Modbus