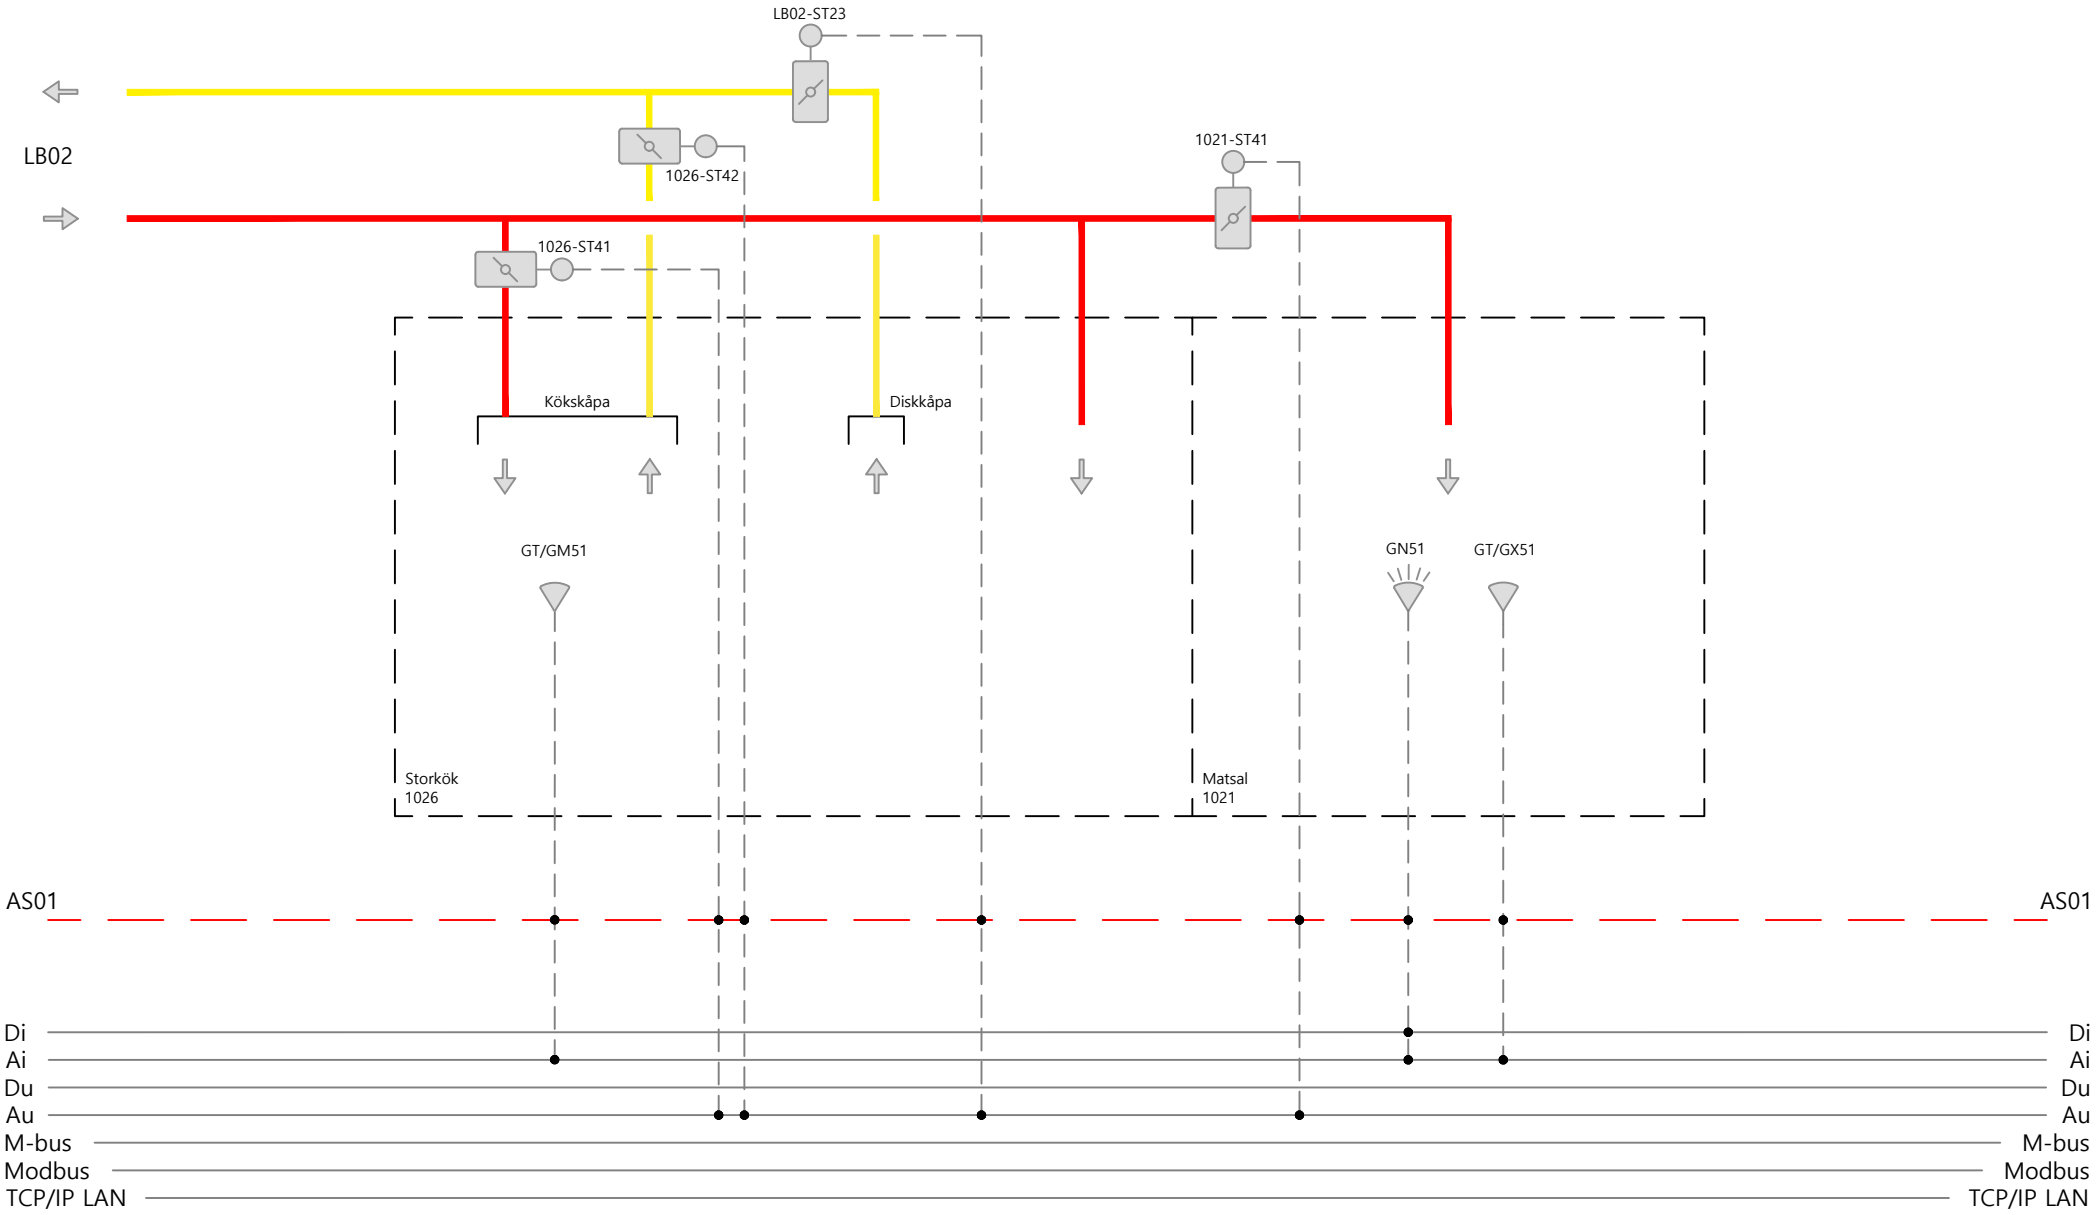
LB02-ST23
LB02
1026-ST42
1021-ST41
1026-ST41
Kökskåpa
Diskkåpa
GT/GM51
GN51
GT/GX51
Storkök
1026
Matsal
1021
AS01
AS01
Di
Ai
Du
Au
M-bus
Modbus
TCP/IP LAN
Di
Ai
Du
Au
M-bus
Modbus
TCP/IP LAN