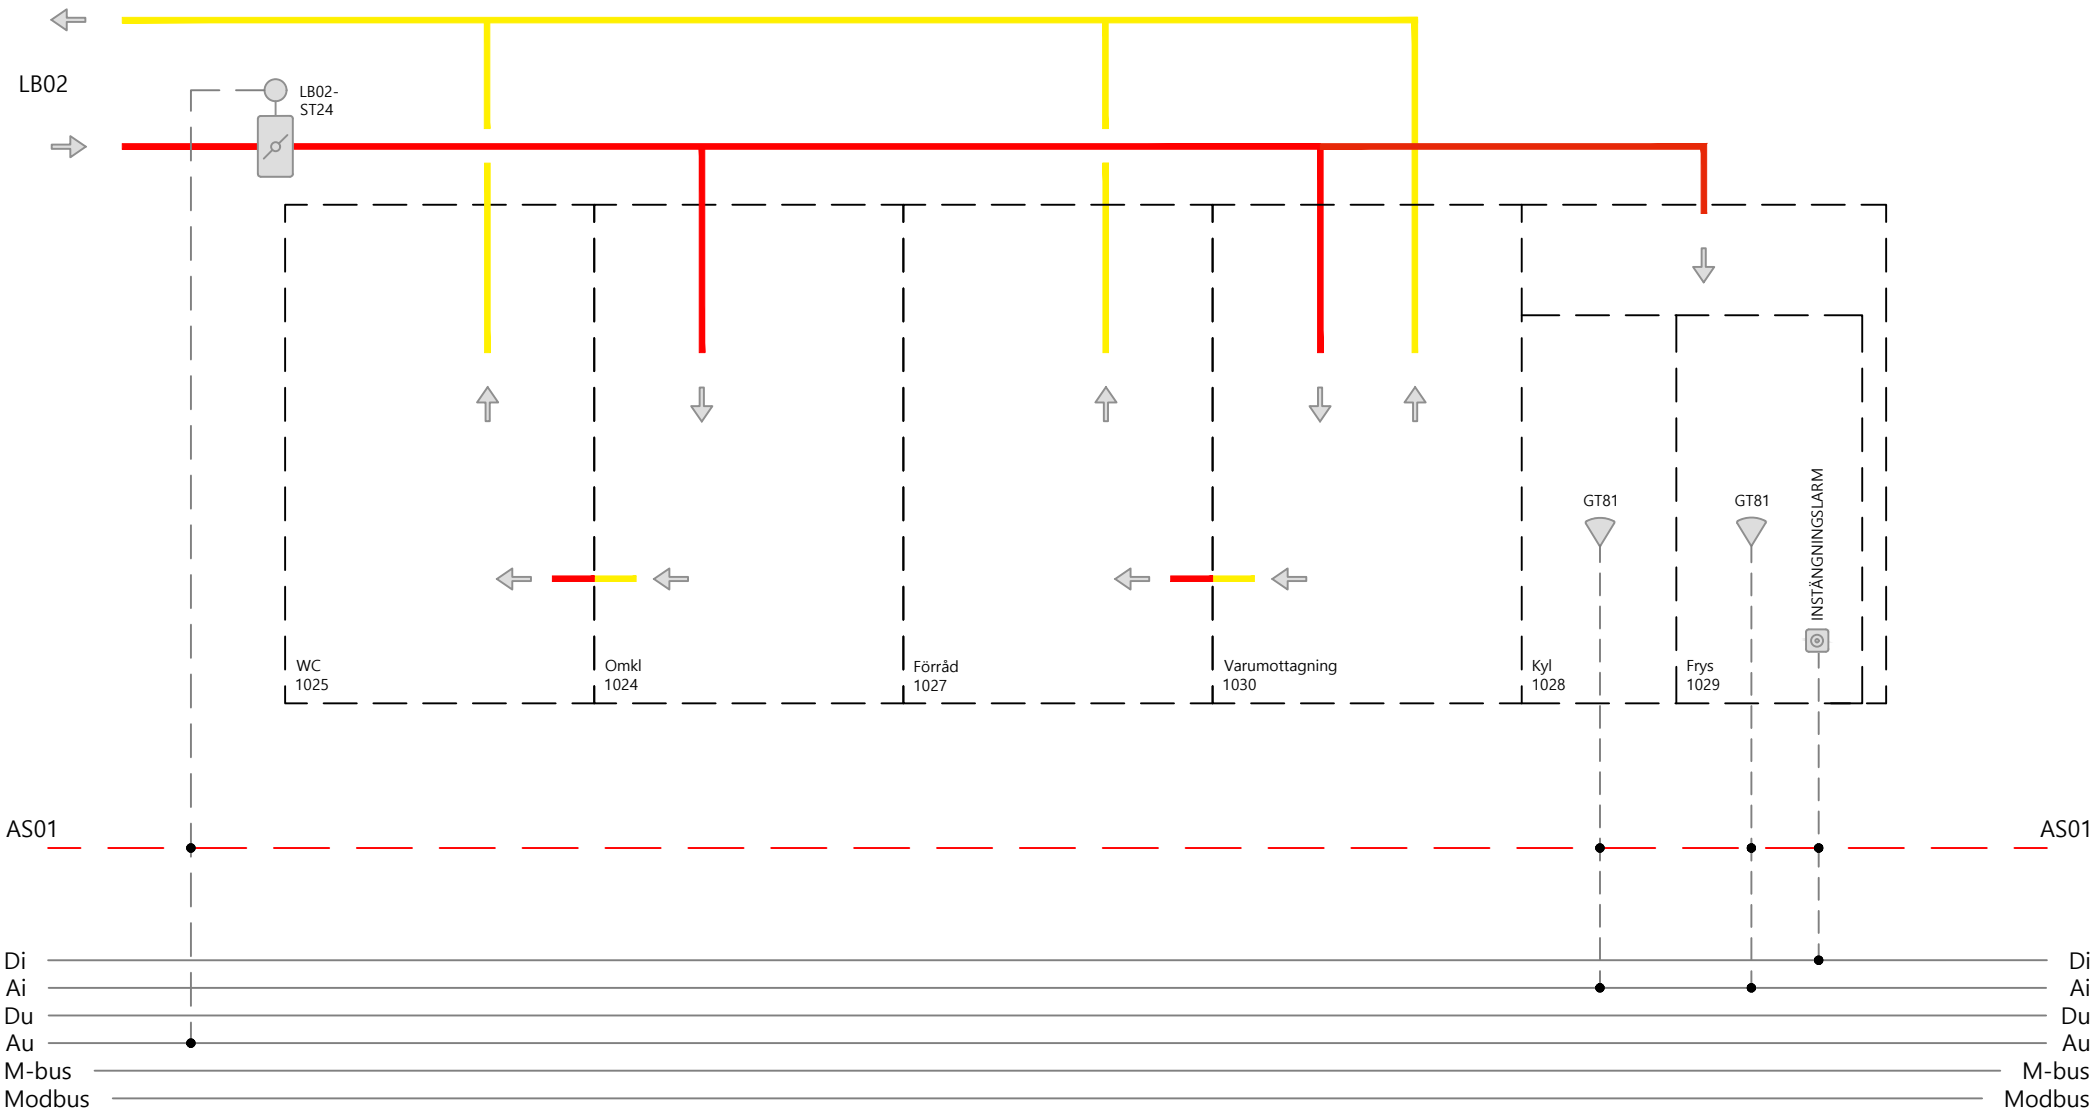
LB02
LB02-
ST24
WC
1025
Omkl
1024
Förråd
1027
Varumottagning
1030
Kyl
1028
Frys
1029
GT81
GT81
INSTÄNGNINGSLARM
AS01
AS01
Di
Ai
Du
Au
M-bus
Modbus
Di
Ai
Du
Au
M-bus
Modbus