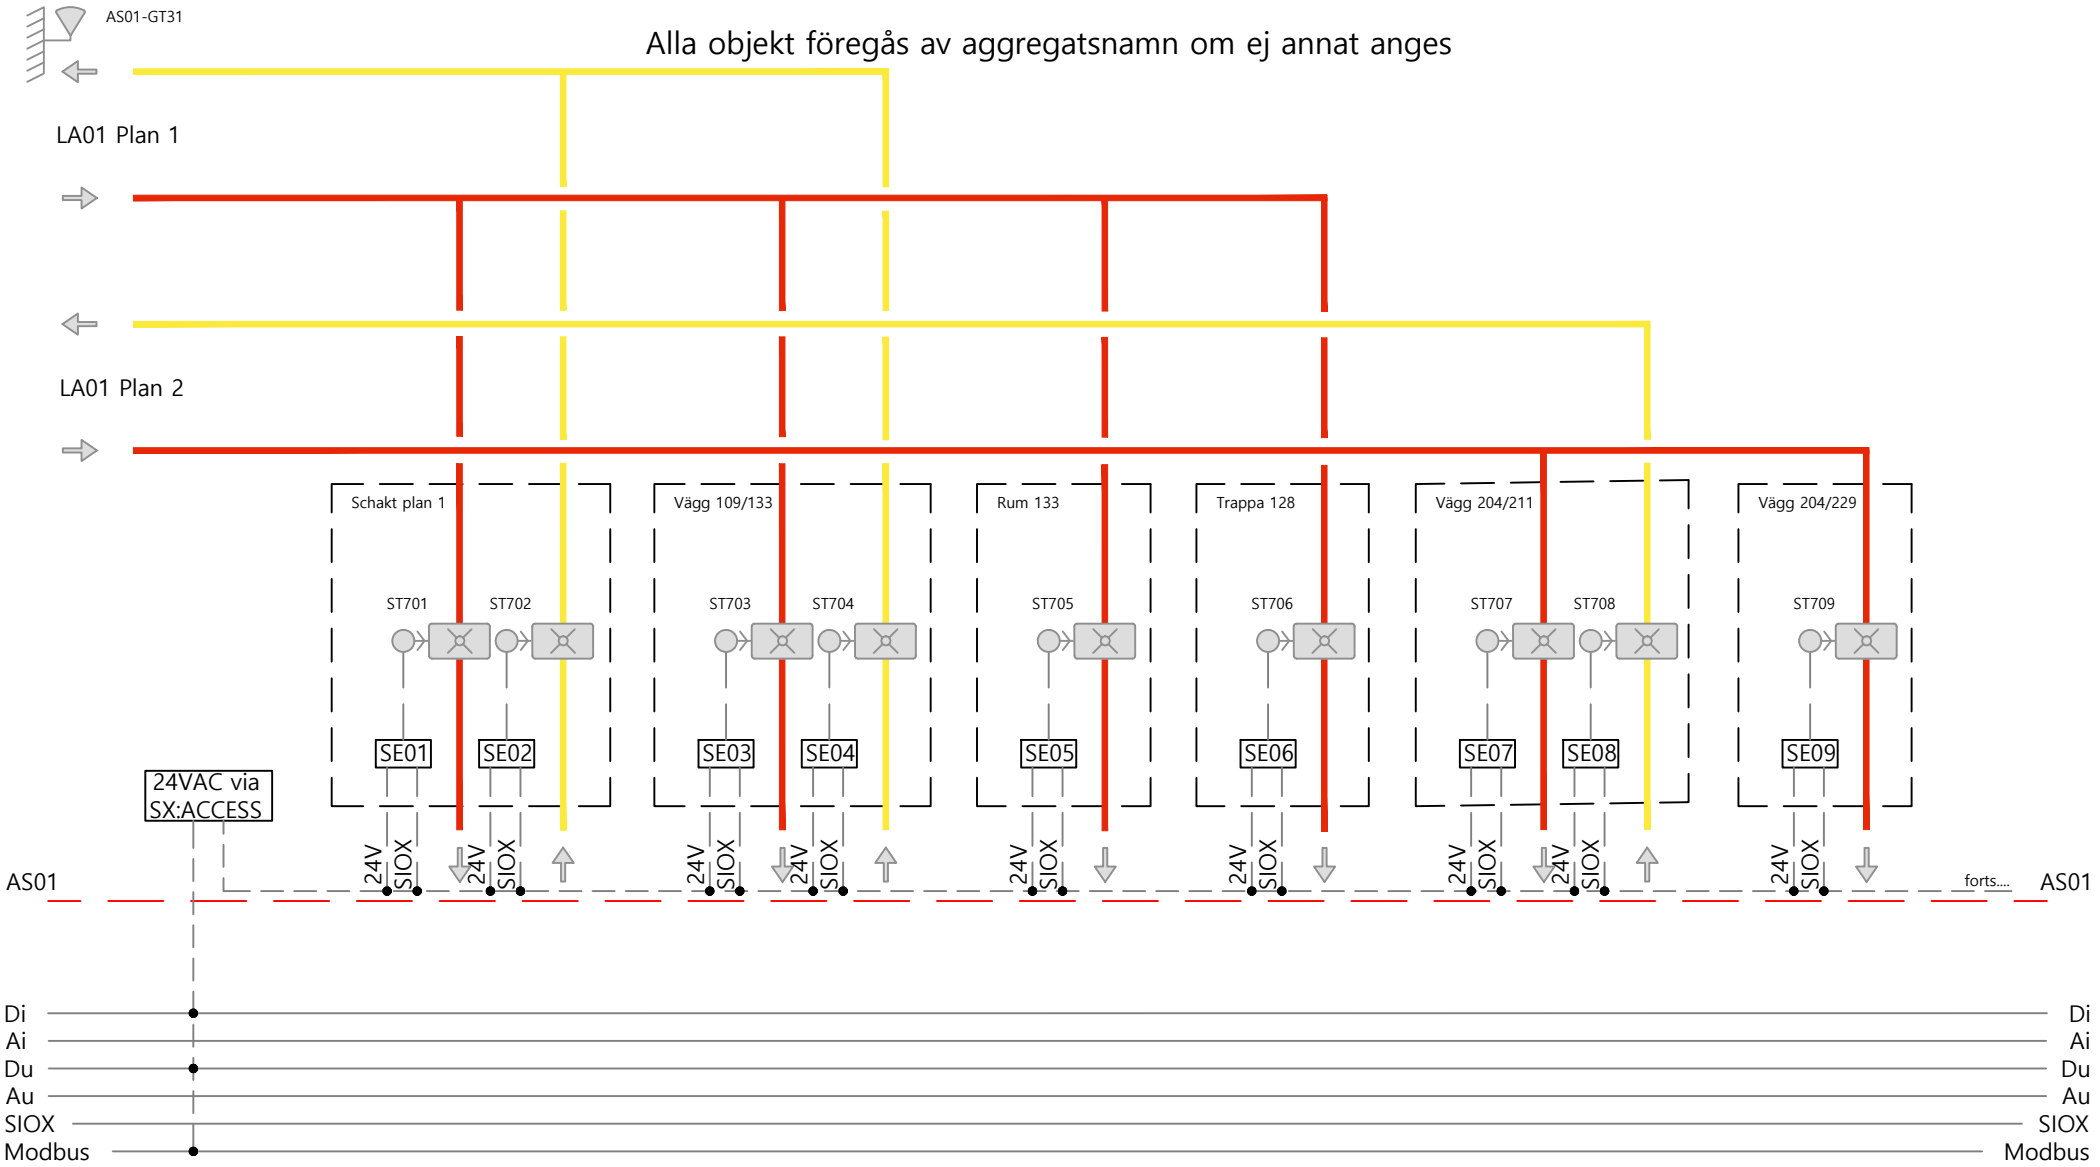

AS01-GT31
Alla objekt föregås av aggregatsnamn om ej annat anges
LA01 Plan 1
LA01 Plan 2
Schakt plan 1
Vägg 109/133
Rum 133
Trappa 128
Vägg 204/211
Vägg 204/229
ST701
ST702
ST703
ST704
ST705
ST706
ST707
ST708
ST709
SE01
SE02
SE03
SE04
SE05
SE06
SE07
SE08
SE09
24V
SIOX
24VAC via
SX:ACCESS
AS01
forts....
AS01
Di
Ai
Du
Au
SIOX
Modbus
Di
Ai
Du
Au
SIOX
Modbus