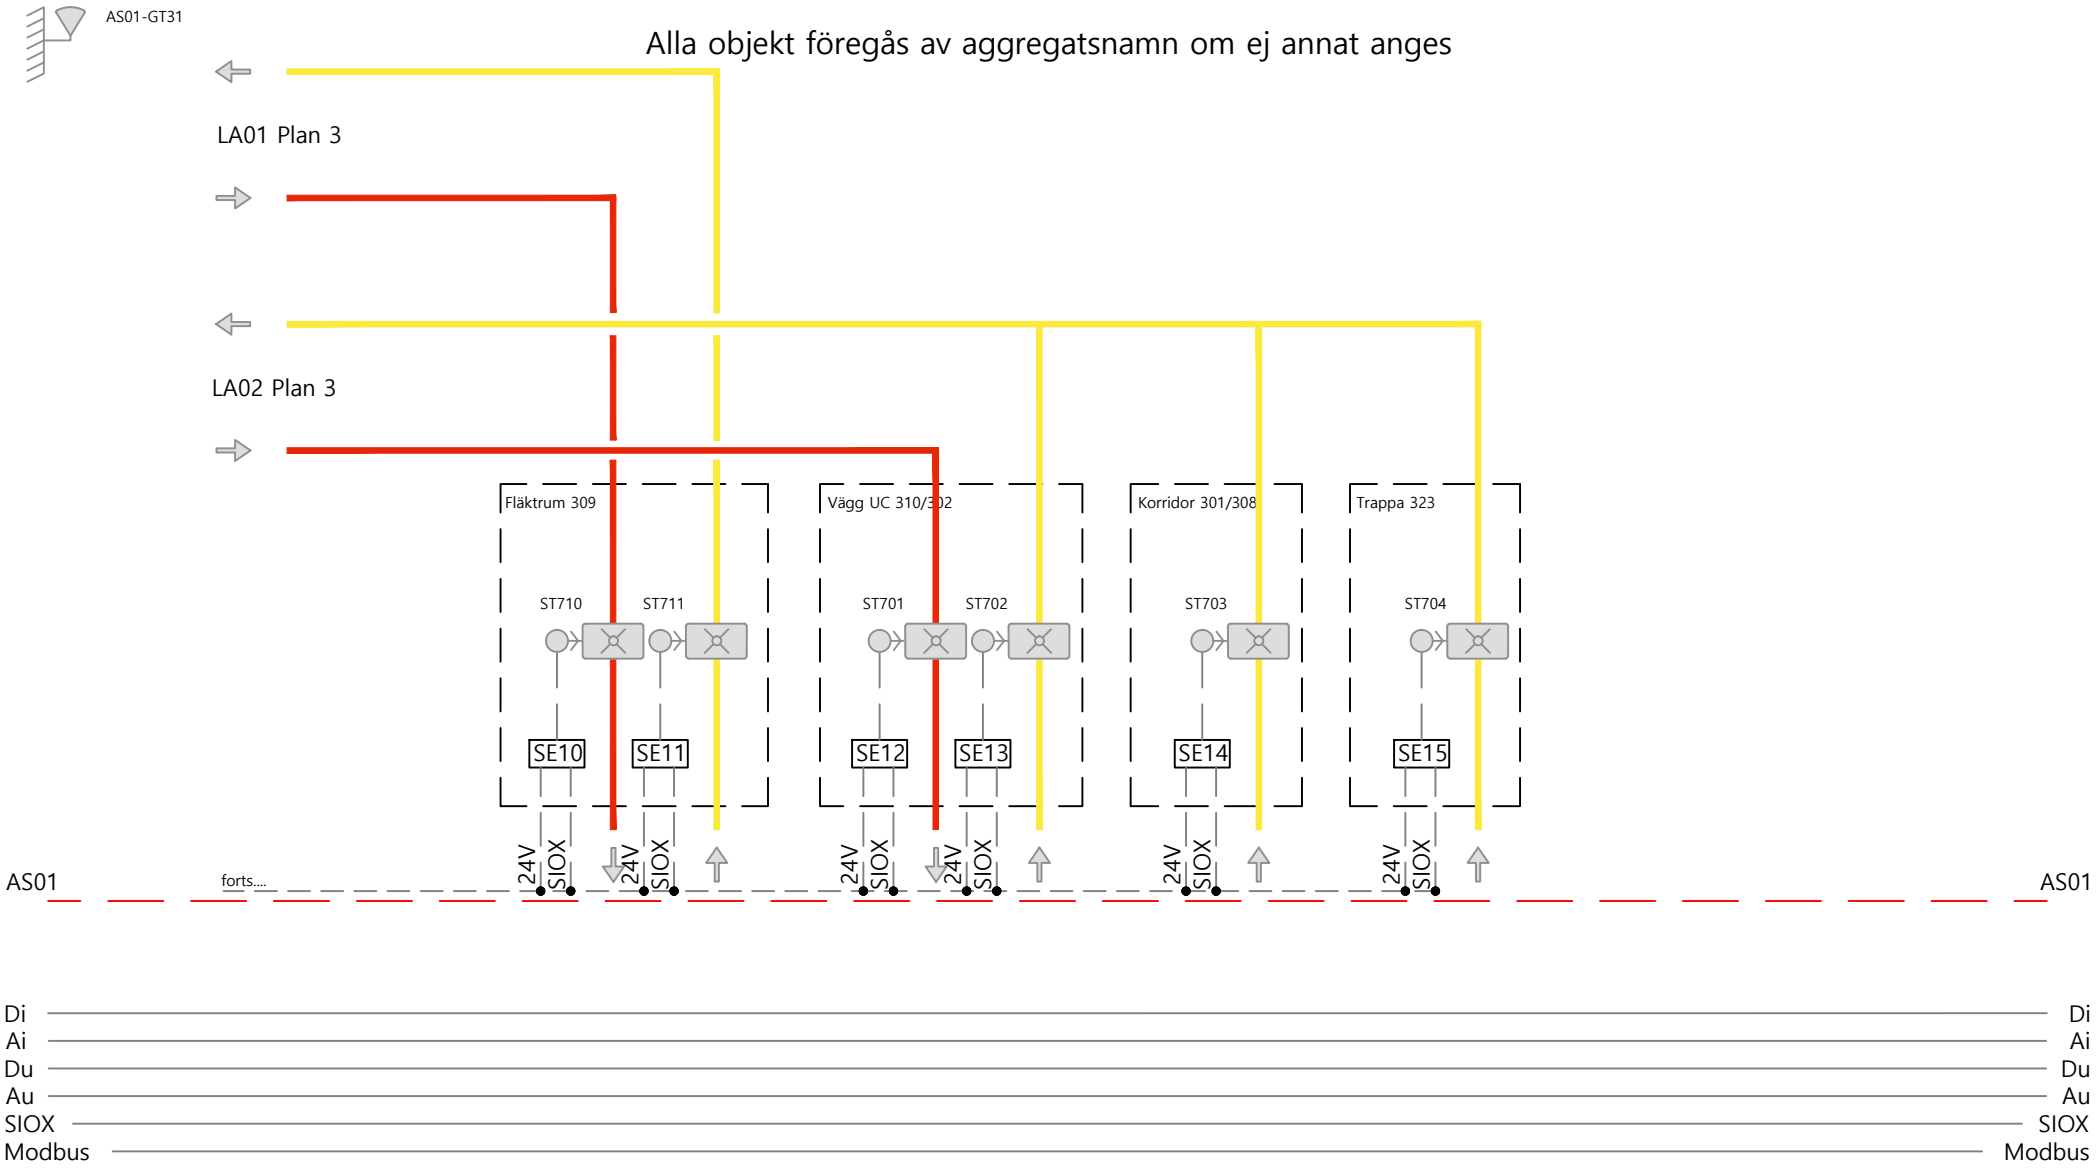
AS01-GT31
Alla objekt föregås av aggregatsnamn om ej annat anges
LA01 Plan 3
LA02 Plan 3
Fläktrum 309
Vägg UC 310/302
Korridor 301/308
Trappa 323
ST710
ST711
ST701
ST702
ST703
ST704
SE10
SE11
SE12
SE13
SE14
SE15
24V
SIOX
AS01
forts....
AS01
Di
Ai
Du
Au
SIOX
Modbus
Di
Ai
Du
Au
SIOX
Modbus