AS01-GT31

Alla objekt föregås av rumsnummer om ej annat anges
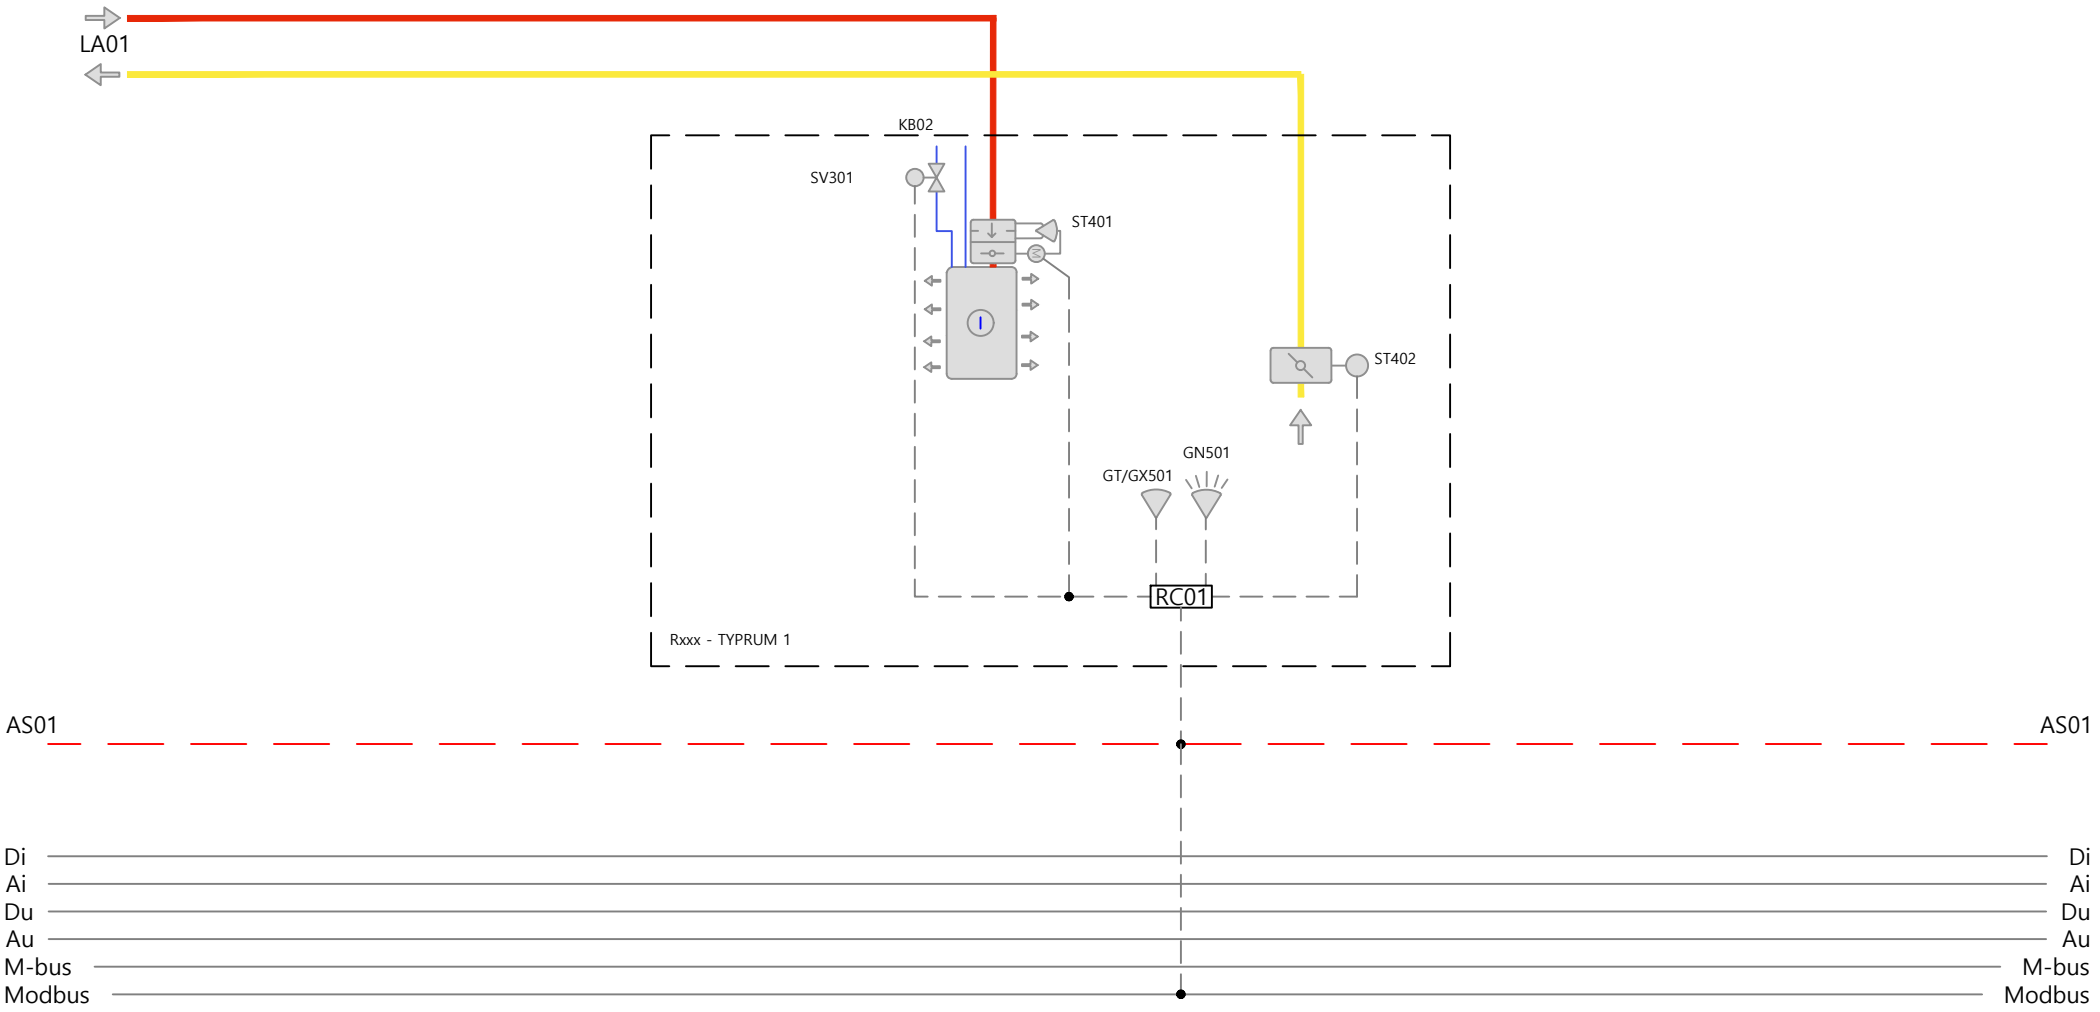
Typrum 1 – Kylbafflar VAV, frånluft VAV