AS01-GT31

Alla objekt föregås av rumsnummer om ej annat anges
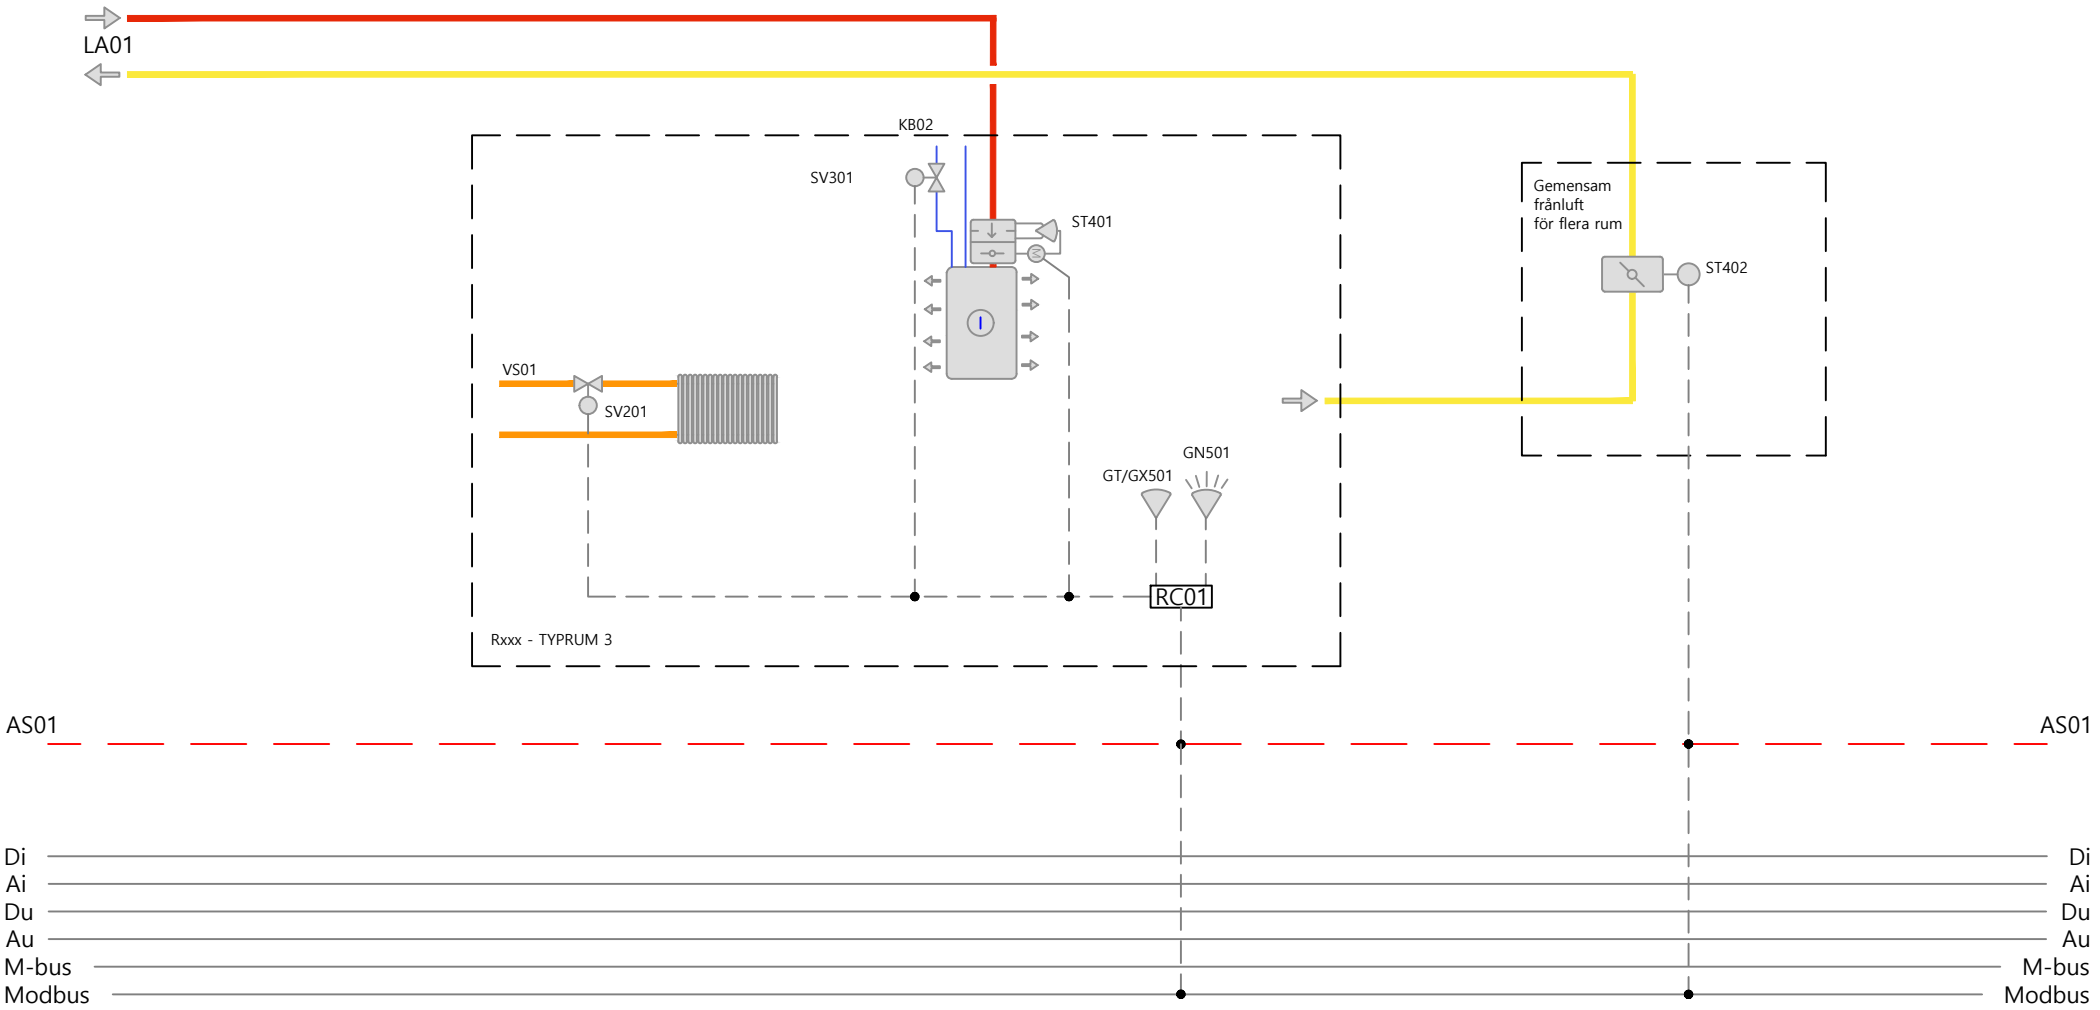
Typrum 3 – Kylbafflar VAV, central frånluft, radiatorer