AS01-GT31

Alla objekt föregås av rumsnummer om ej annat anges
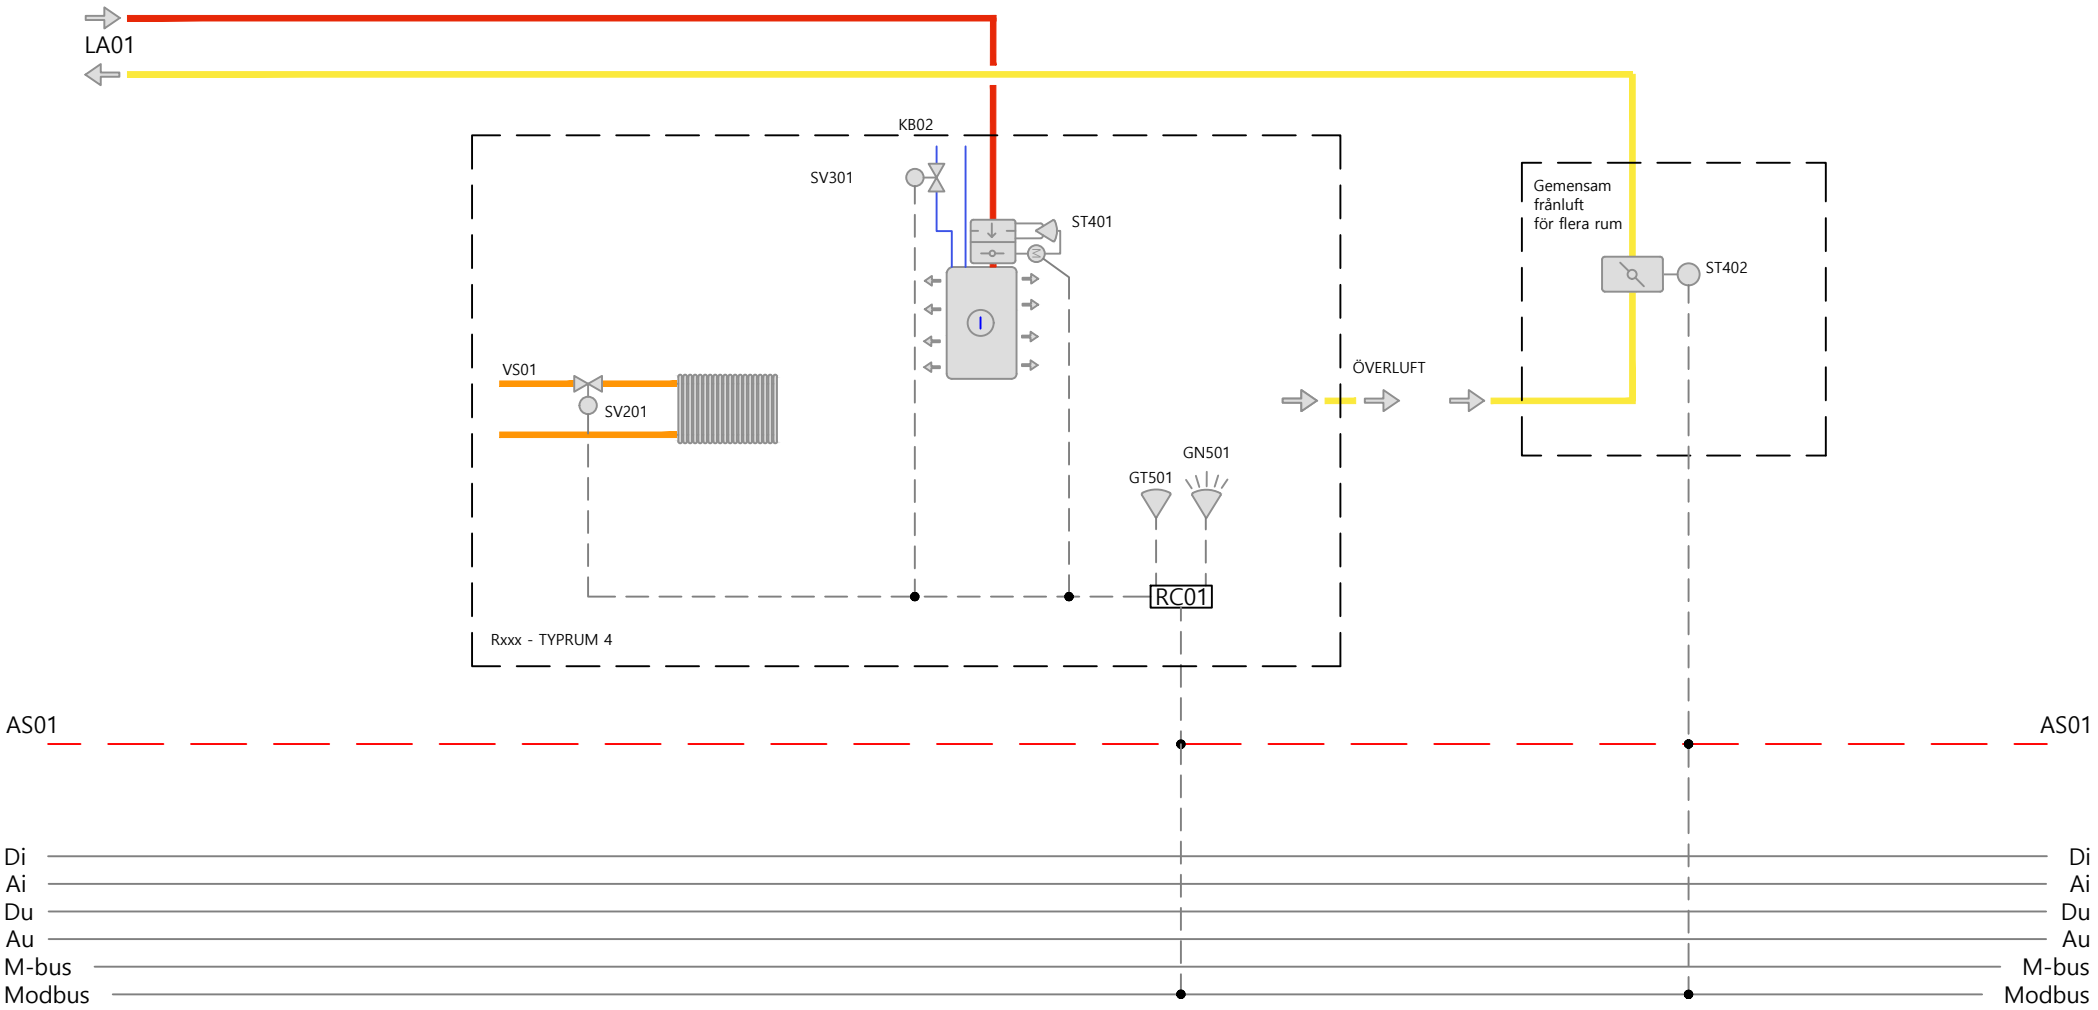
Typrum 4 – Kylbafflar VAV, överluft, radiatorer