AS01-GT31

# Alla objekt föregås av rumsnummer om ej annat anges
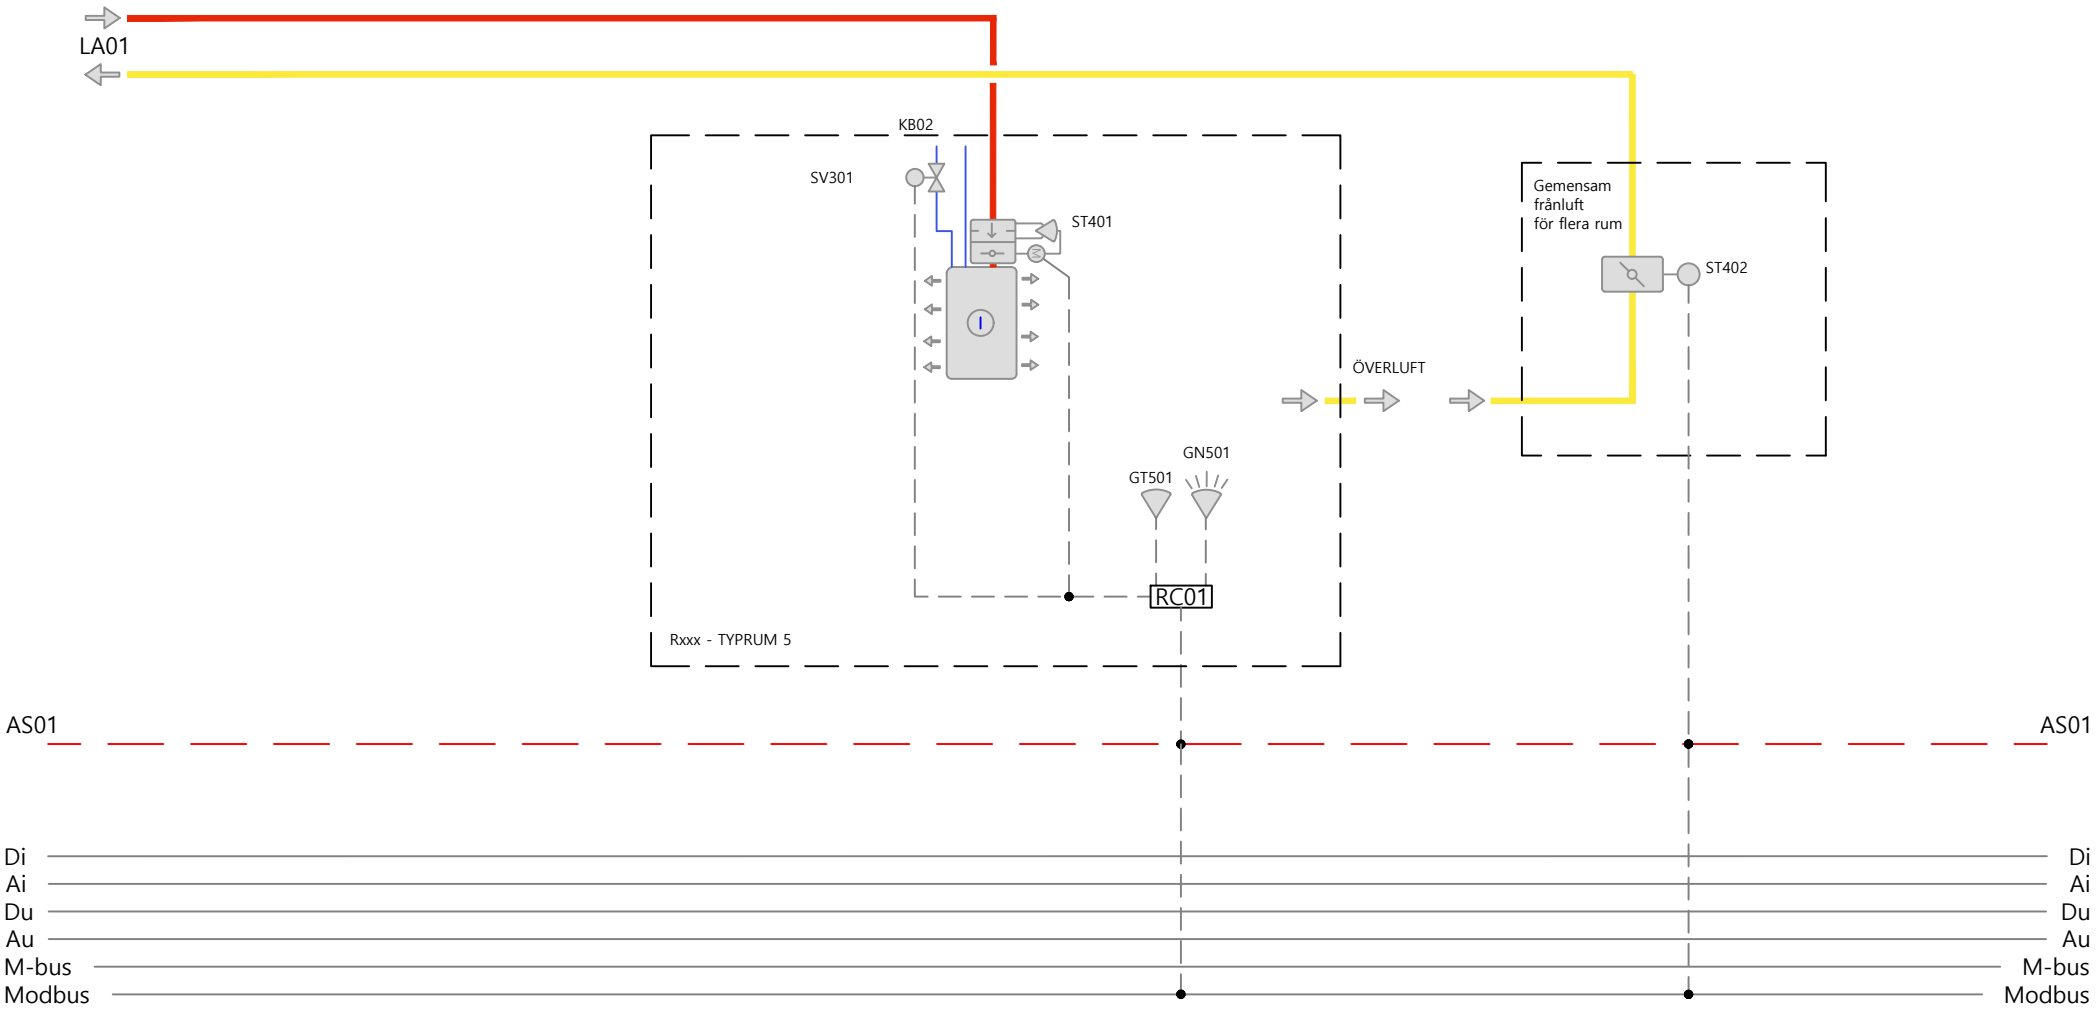
Typrum 5 – Kylbafflar VAV, överluft