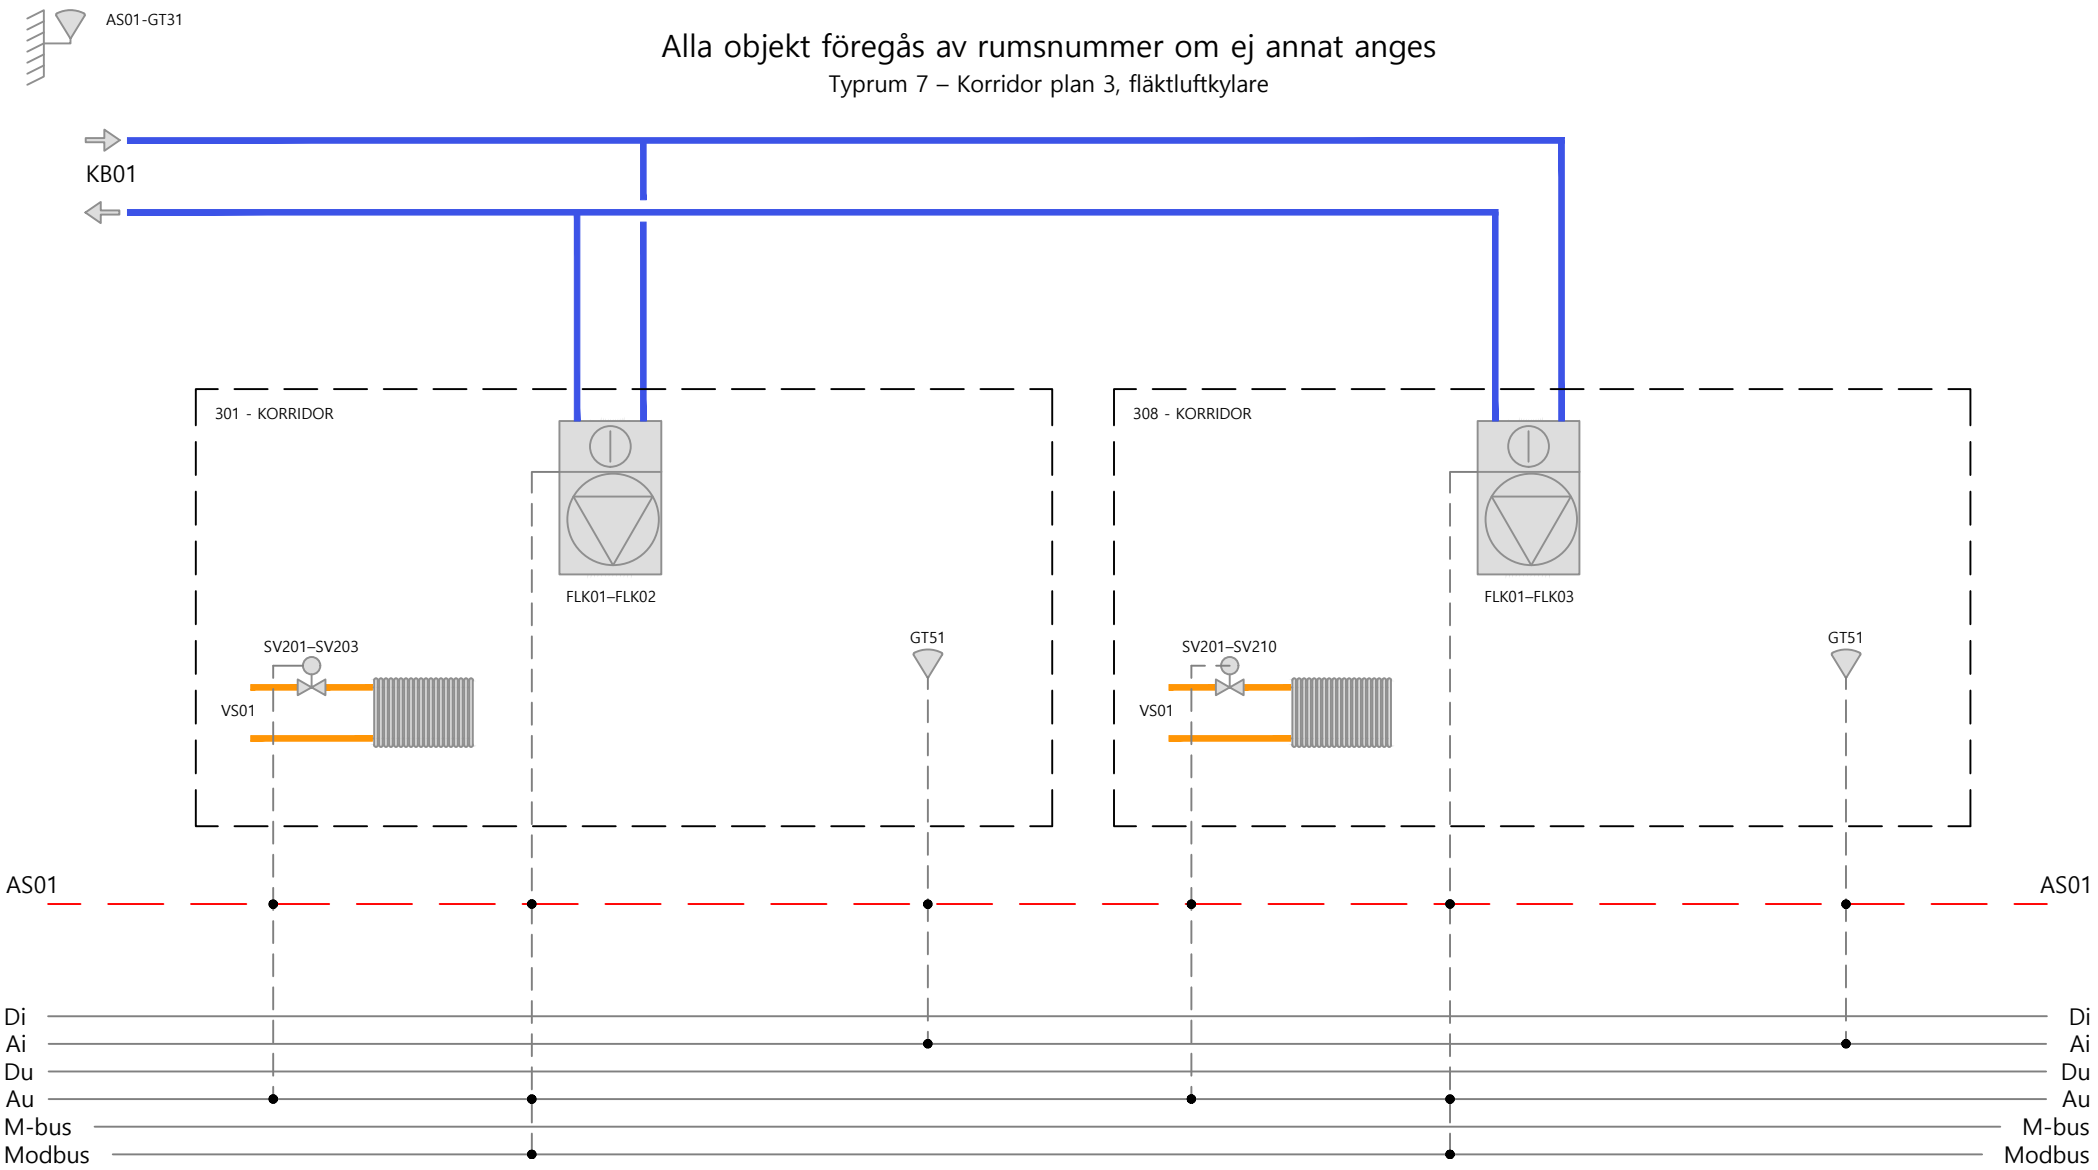

AS01-GT31
Alla objekt föregås av rumsnummer om ej annat anges
Typrum 7 – Korridor plan 3, fläktluftkylare
KB01
301 - KORRIDOR
FLK01–FLK02
SV201–SV203
VS01
GT51
308 - KORRIDOR
FLK01–FLK03
SV201–SV210
VS01
GT51
AS01
AS01
Di
Ai
Du
Au
M-bus
Modbus
Di
Ai
Du
Au
M-bus
Modbus